PROPOSED RESIDENTIAL ONE BEDROOM BLOCK OF FLAT,MABUSHI

STRUCTURAL DRAWINGS

JANUARY, 2021

Structural Engineers

TAPES CONSTRUCTION

GENERAL NOTES

A. THIS DRAWING IS TO BE READ IN CONJUNCTION WITH ALL RELEVANT ARCHITECTURAL, MECHANICAL AND ELECTRICAL DRAWINGS.

B. THE CONTRACTOR IS TO CONFIRM THE POSITION OF PERMANENT FIXTURES, CONDUITS AND HOLES ACCORDING TO THE ARCHITECTURAL, MECHANICAL AND ELECTRICAL DRAWINGS.

C. ALL DIMENSIONS ARE IN MILLIMETRES UNLESS OTHERWISE STATED. DO NOT SCALE DRAWINGS, IF IN DOUBT CALL ATTENTION OF ENGINEER.

D. GRADE 25 CONCRETE (NOMINAL MIX 1:2:3) WITH 28 DAY CUBE STRENGTH OF 25N/mm2 IS TO BE USED FOR ALL CONCRETE BEAMS & COLUMNS.

E. GRADE 20 CONCRETE (NOMINAL MIX 1:2:4) WITH 28 DAY CUBE STRENGTH OF 20N/mm2 IS TO BE USED FOR ALL CONCRETE SLABS.

F. GRADE 15 CONCRETE (NOMINAL MIX 1:2:6) WITH 28 DAY CUBE STRENGTH OF 15N/mm2 IS TO BE USED FOR ALL MASS CONCRETE WORKS.

G. CRUSHED ROCKS AGGREGATES WITH A MAXIMUM SIZE OF 20mm IS TO BE USED FOR ALL CONCRETE WORKS.

H. NOMINAL COVER TO REINFORCEMENT IN FOUNDATION, COLUMNS, BEAMS AND SLABS SHALL BE 50mm, 40mm, 30mm and 20mm RESPECTIVELY.

I. THE SYMBOLS 'Y' AND 'R' DENOTES HIGH YIELD DEFORMED BARS TO BS 4461 AND MILD STEEL BARS TO BS 4449 RESPECTIVELY.

J. THE CHARACTERISTIC STRENGTH OF HIGH YIELD STEEL BARS AND MILD STEEL BARS SHALL BE 410N/mm2 AND 250N/mm2 RESPECTIVELY.

K. THE FOUNDATION HAS BEEN DESIGNED FOR AN ASSUMED SOIL BEARING CAPACITY OF 150KN/m2

L. FOR LINTELS LESS THAN 2.0m SPAN USE 2Y12 TOP AND BOTTOM & Y8@300 c/c AS STIRRUP. FOR LINTELS WITH SPAN GREATER THAN 2.0m USE 2Y16 BOTTOM & 2Y12 TOP & Y8@300 c/c AS STIRRUP.

M. ALL STRUCTURAL CONNECTION SHALL BEDONE ACCORDING TO ENGINEERS INSTRUCTION. SEEK ENGINEERS ATTENTION IN CASE OF ANY DOUBT. 2Y16 BOTTOM & 2Y12 TOP & Y8@300 c/c AS STIRRUP.

N. A WIND SPEED OF 36m/s HAS BEEN USED FOR WIND ANALYSIS.

O. THE STRUCTURAL ENGINEER SHALL NOT BE HELD RESPONSIBLE FOR CONSTRUCTION WORKS NOT SUPERVISED BY HIM.

CLIENT	PROJECT	DRG. TITLE					
Alh. AHMED JIBRIL AHMED	PROPOSED RESIDENTIAL ONE BEDROOM BLOCK OF FLAT, MABUSHI	GENERAL NOTES	MARK	DATE	MADE BY	REVISIONS	

TAPES CONSTRUCTION
NO 365 SHARADA PHASE 1
KANO, KANO STATE

JOB NO	A A BINDAWA DESIGNED	A A BINDAWA DRAWN	00 DRG. No
FREE SCALE:	ENGR. J K CHECKED:	JAN, 2021 DATE:	REV.

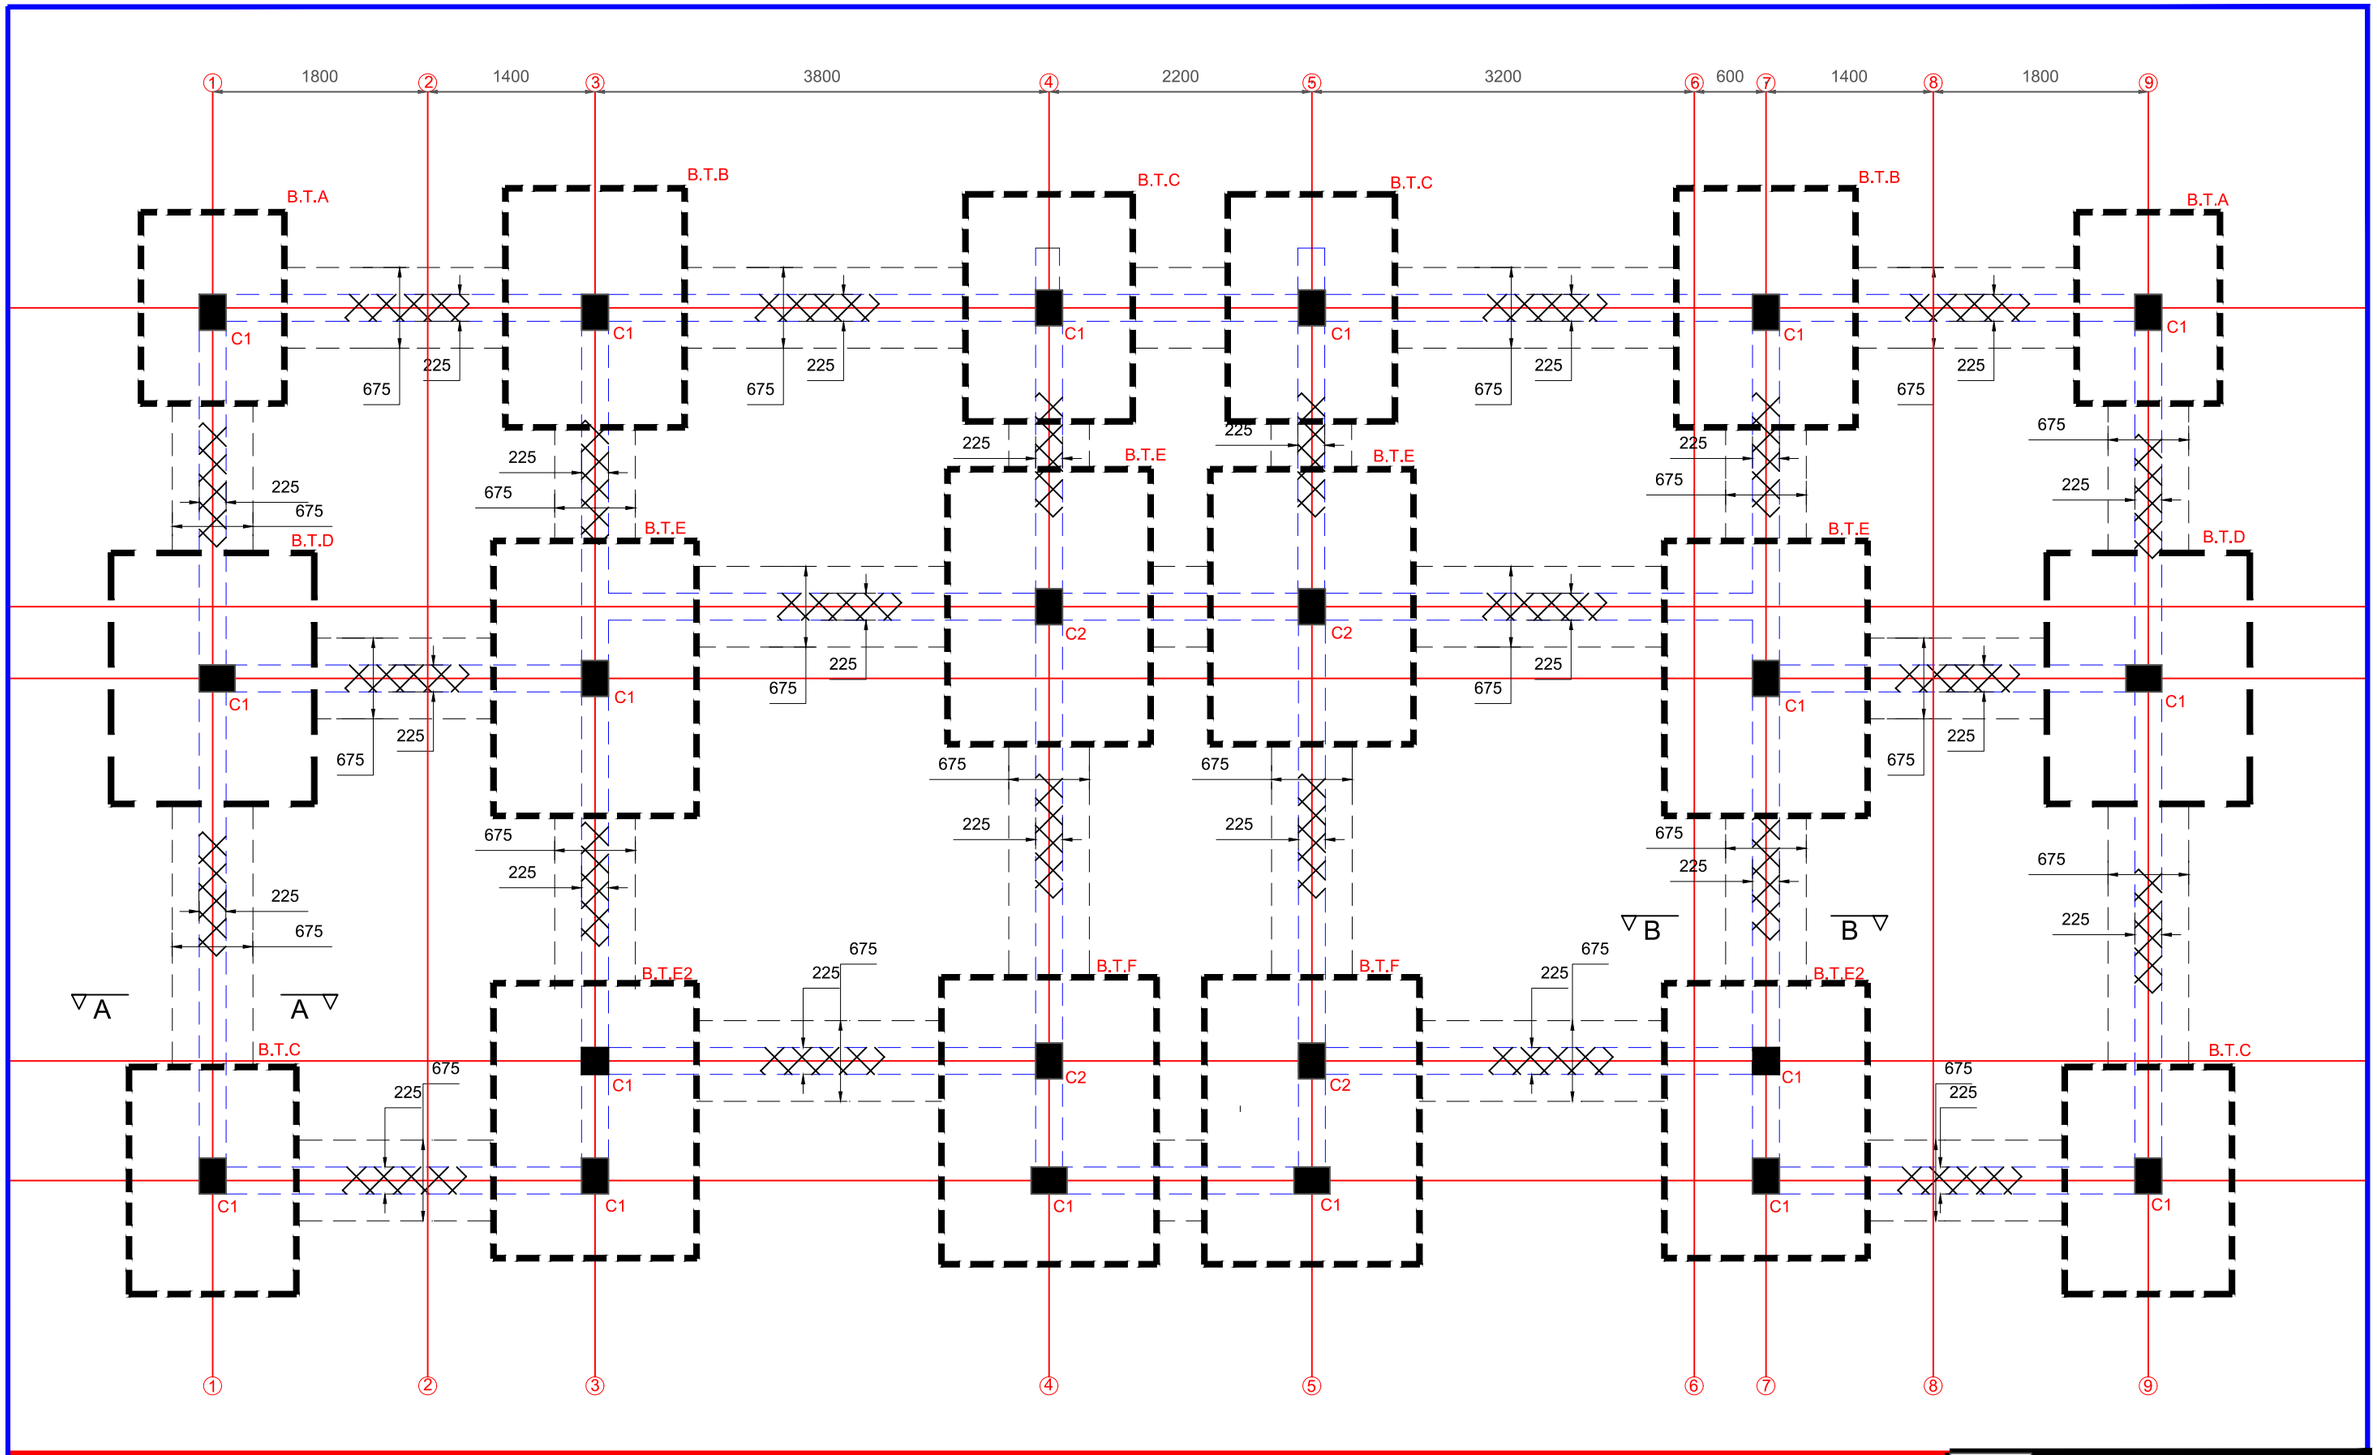

CLIENT	PROJECT	DRG. TITLE
Alh. AHMED JIBRIL AHMED	PROPOSED RESIDENTIAL ONE BEDROOM BLOCK OF FLAT, MABUSHI.	FOUNDATION LAYOUT

MARK	DATE	MADE BY	REVISIONS

TAPES CONSTRUCTION
NO 365 SHARADA PHASE 1
KANO, KANO STATE

JOB NO	DESIGNED	DRAWN	DRG. No
	A A BINDAWA	A A BINDAWA	001
SCALE: FREE	CHECKED: ENGR. J K	DATE: JAN, 2021	REV. 01

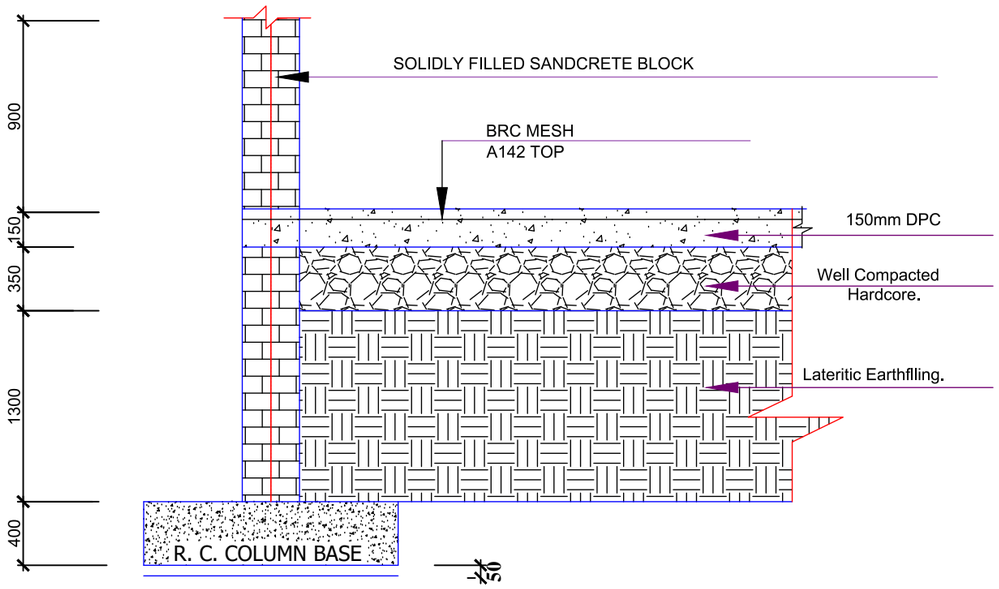

SECTION A-A

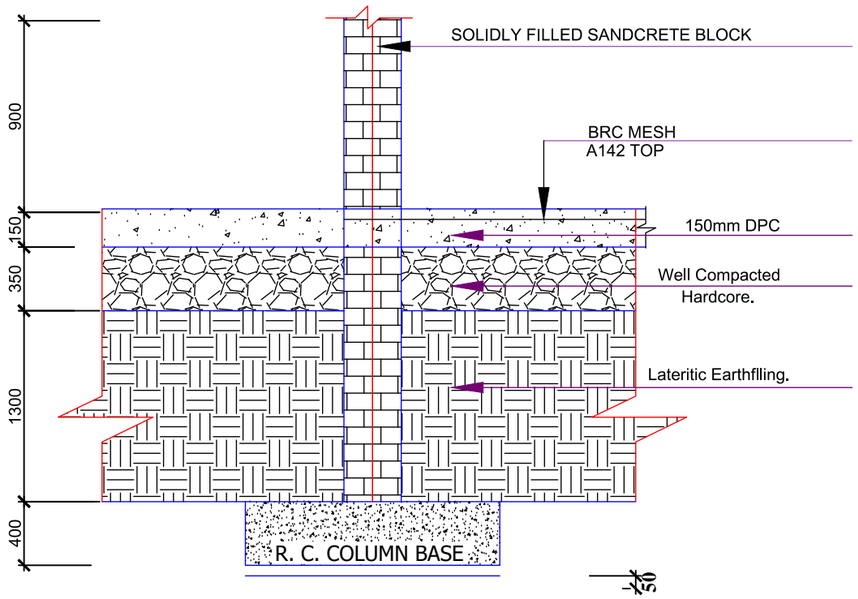

SECTION B-B

CLIENT	PROJECT	DRG. TITLE
Alh. AHMED JIBRIL AHMED	PROPOSED RESIDENTIAL ONE BEDROOM BLOCK OF FLAT, MABUSHI.	SECTION THROUGH FOUNDATION FLOOR

MARK	DATE	MADE BY	REVISIONS

TAPES CONSTRUCTION
NO 365 SHARADA PHASE 1
KANO, KANO STATE

JOB NO	DESIGNED	DRAWN	DRG. No
	A A BINDAWA	A A BINDAWA	002
SCALE: FREE	CHECKED: ENGR. J K	DATE: JAN, 2021	REV. 01

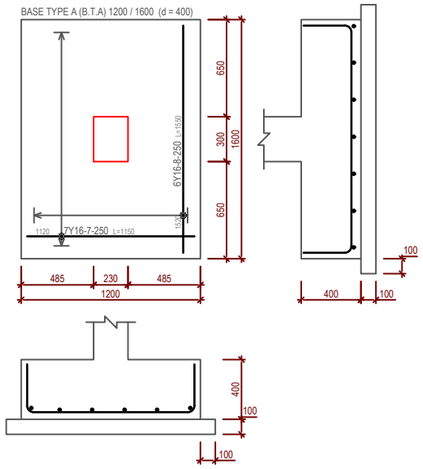

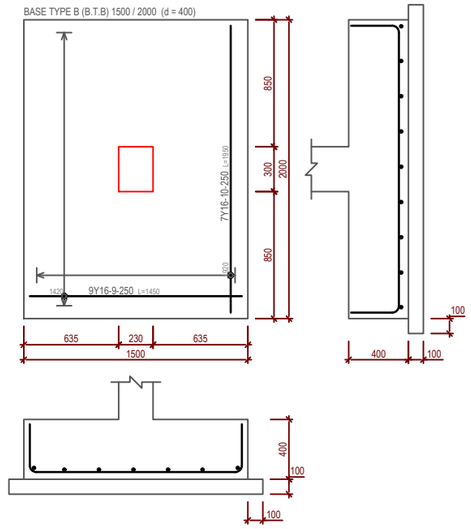

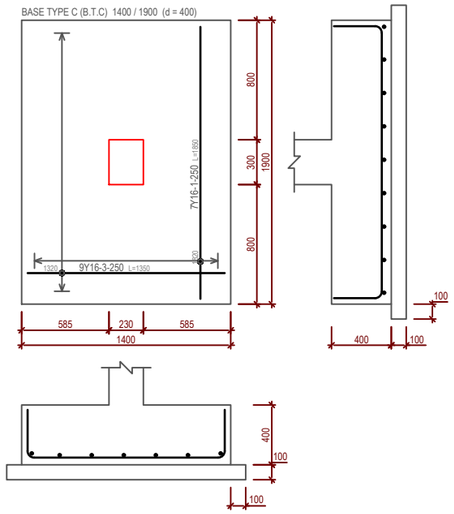

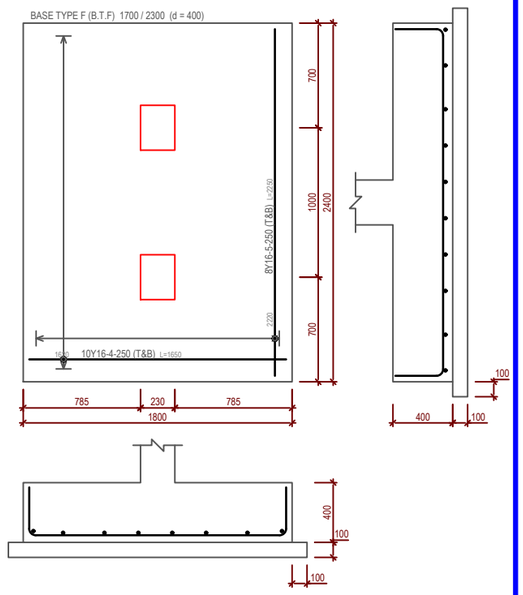

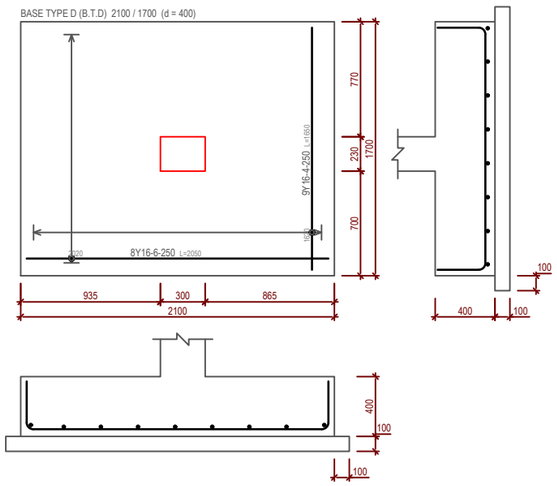

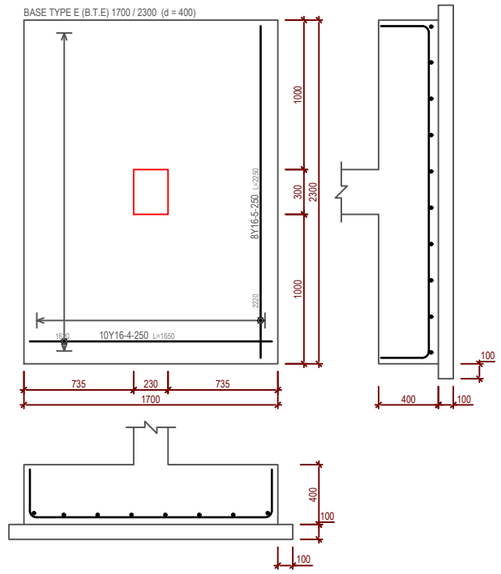

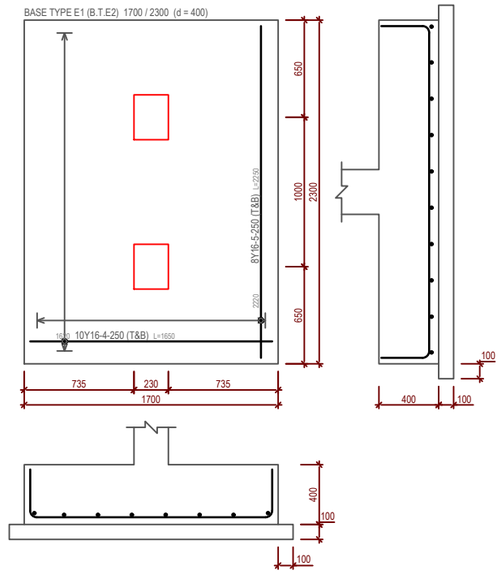

CLIENT	PROJECT	DRG. TITLE
Alh. AHMED JIBRIL AHMED	PROPOSED RESIDENTIAL ONE BEDROOM BLOCK OF FLAT, MABUSHI.	FOOTING REINFORCEMENT DETAILS

MARK	DATE	MADE BY	REVISIONS

TAPES CONSTRUCTION
NO 365 SHARADA PHASE 1
KANO, KANO STATE

JOB NO	DESIGNED	DRAWN	DRG. No
	A A BINDAWA	A A BINDAWA	003
SCALE: FREE	CHECKED: ENGR. J K	DATE: JAN, 2021	REV. 01

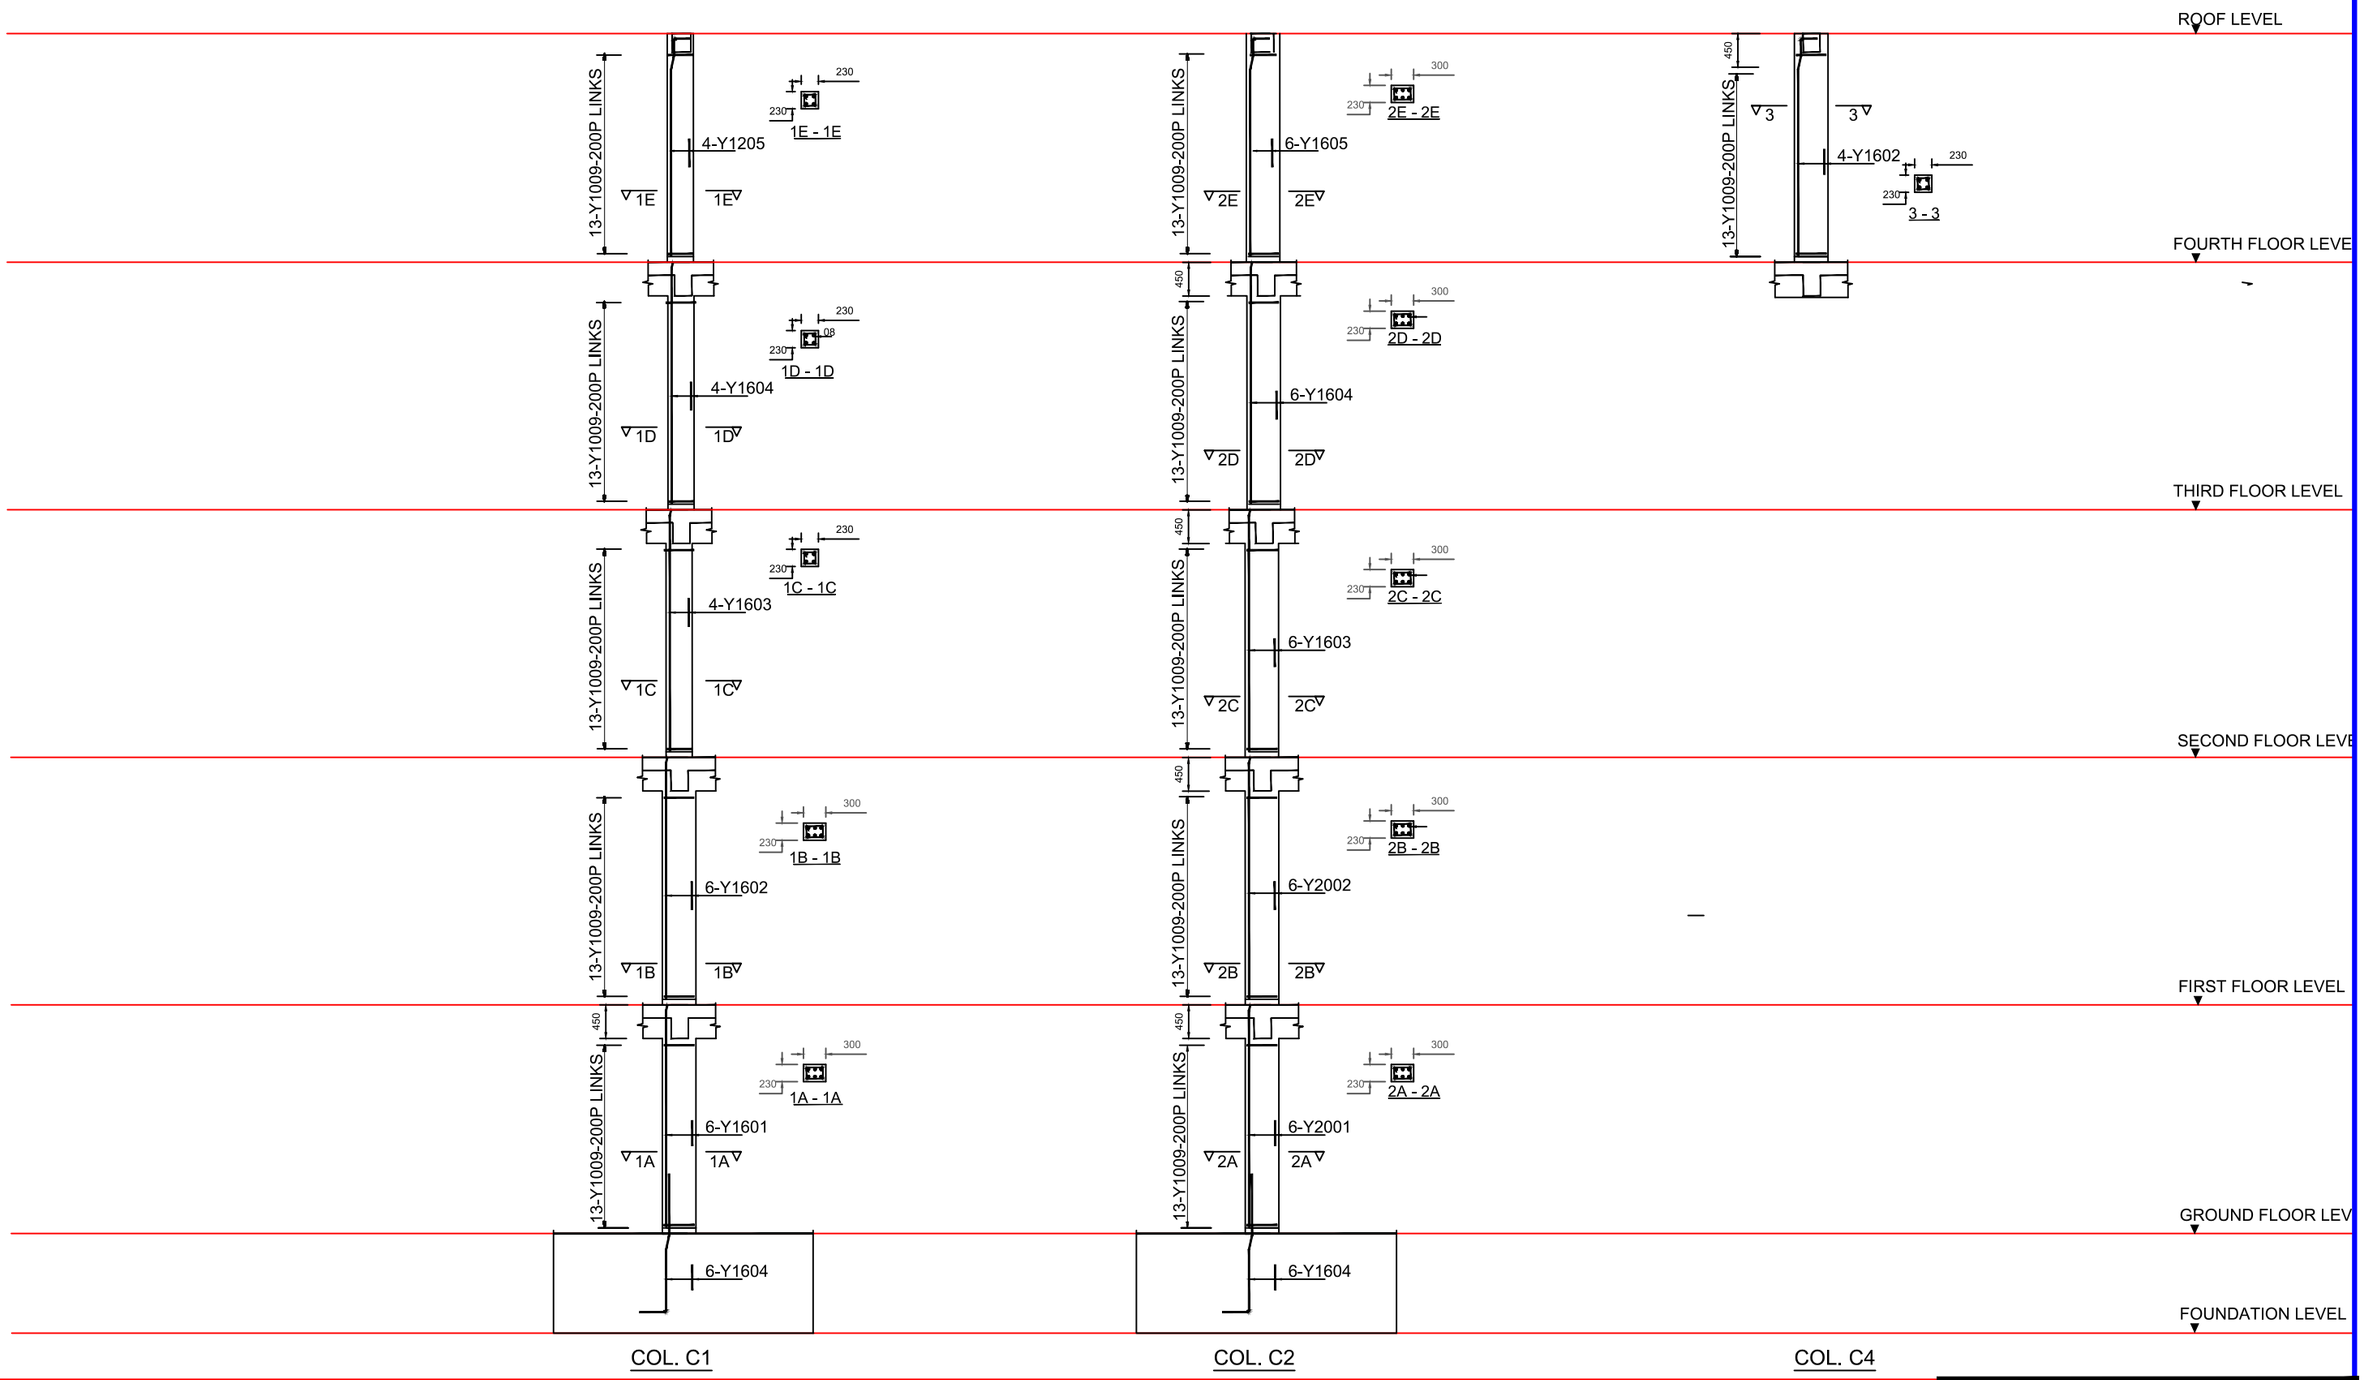

CLIENT	PROJECT	DRG. TITLE
Alh. AHMED JIBRIL AHMED	PROPOSED RESIDENTIAL ONE BEDROOM BLOCK OF FLAT, MABUSHI.	COLUMNS REINF. DETAILS AND SECTIONS

MARK	DATE	MADE BY	REVISIONS

TAPES CONSTRUCTION
NO 365 SHARADA PHASE 1
KANO, KANO STATE

JOB NO	DESIGNED	DRAWN	DRG. No
	A A BINDAWA	A A BINDAWA	004
SCALE: FREE	CHECKED: ENGR. J K	DATE: JAN, 2021	REV. 01

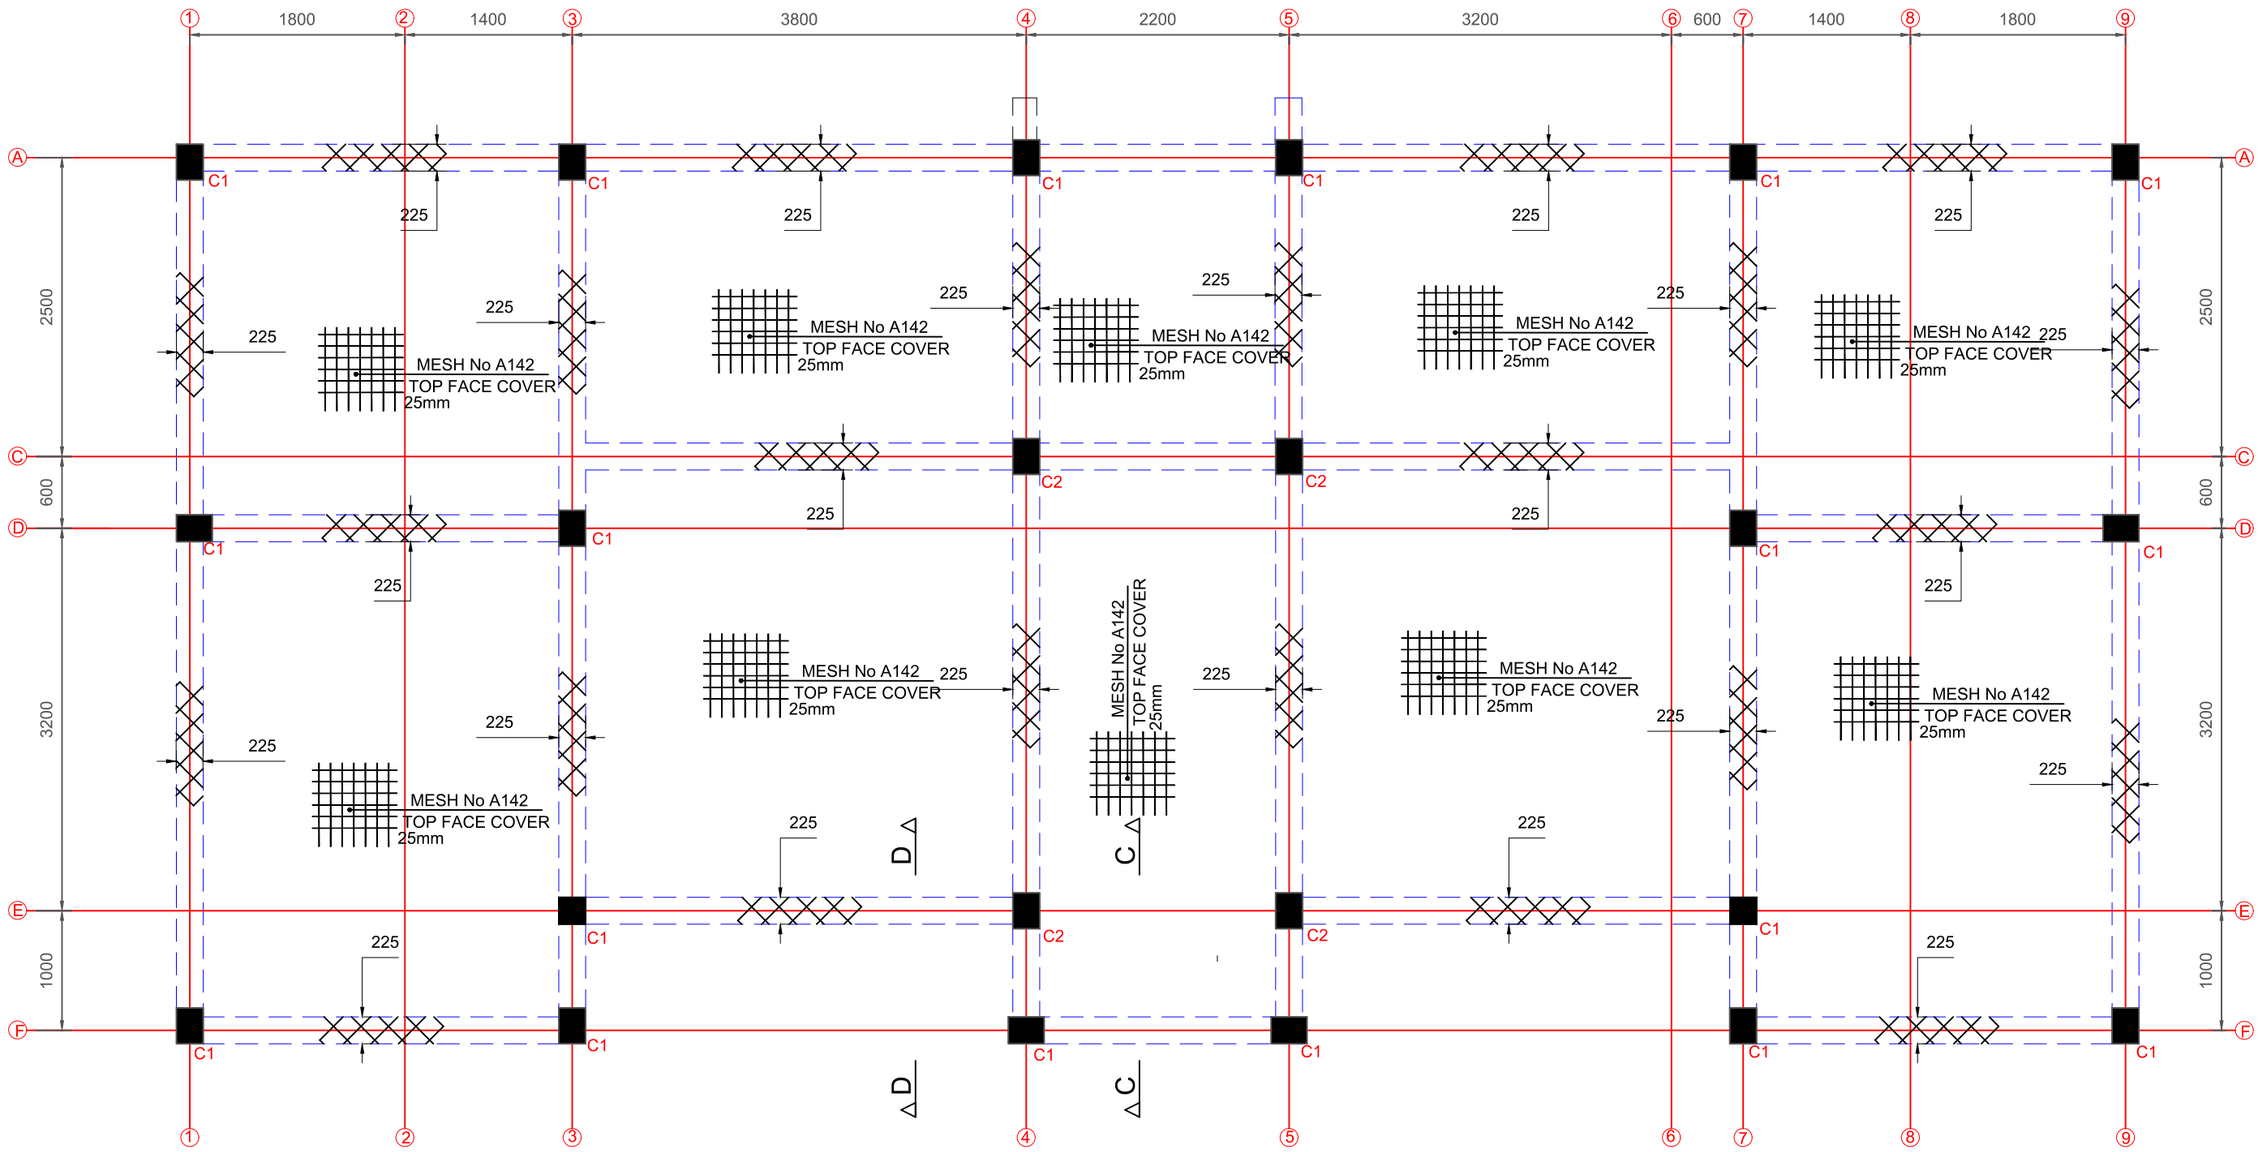

CLIENT	PROJECT	DRG. TITLE
Alh. AHMED JIBRIL AHMED	PROPOSED RESIDENTIAL ONE BEDROOM BLOCK OF FLAT, MABUSHI.	GROUND FLOOR LAYOUT

MARK	DATE	MADE BY	REVISIONS

TAPES CONSTRUCTION
NO 365 SHARADA PHASE 1
KANO, KANO STATE

JOB NO	DESIGNED	DRAWN	DRG. No
	A A BINDAWA	A A BINDAWA	005
SCALE; FREE	CHECKED; ENGR. J K	DATE; JAN, 2021	REV. 01

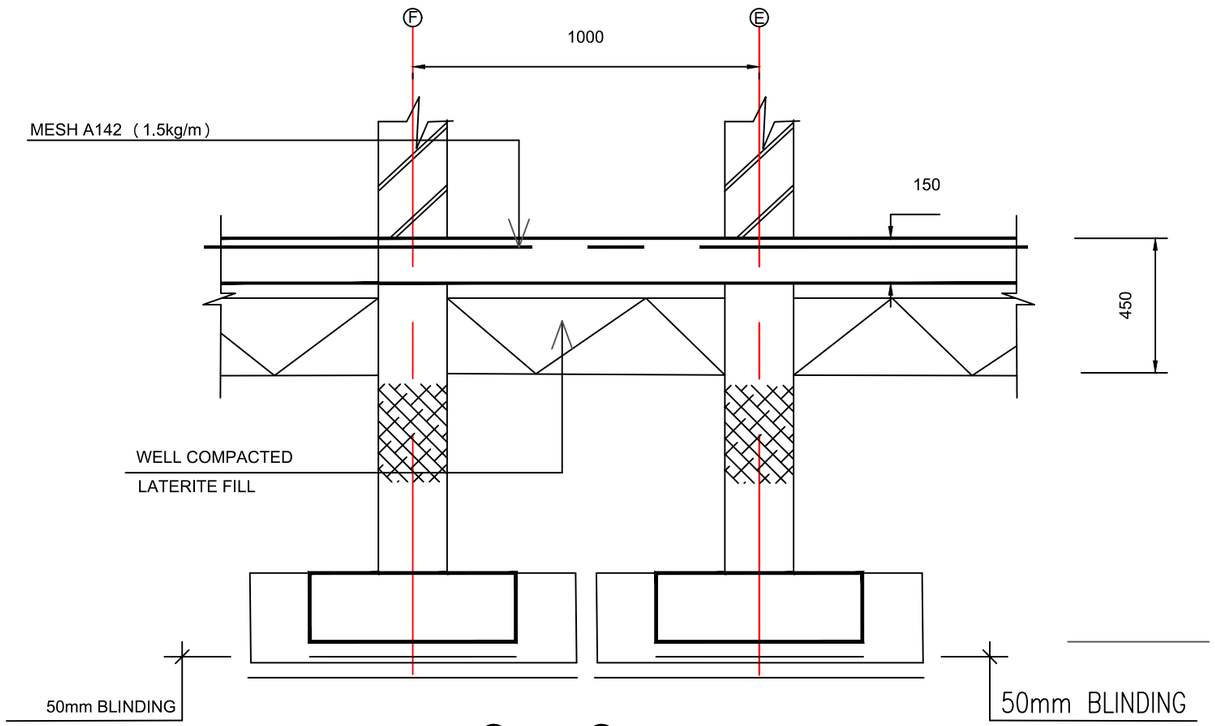

3 - 3

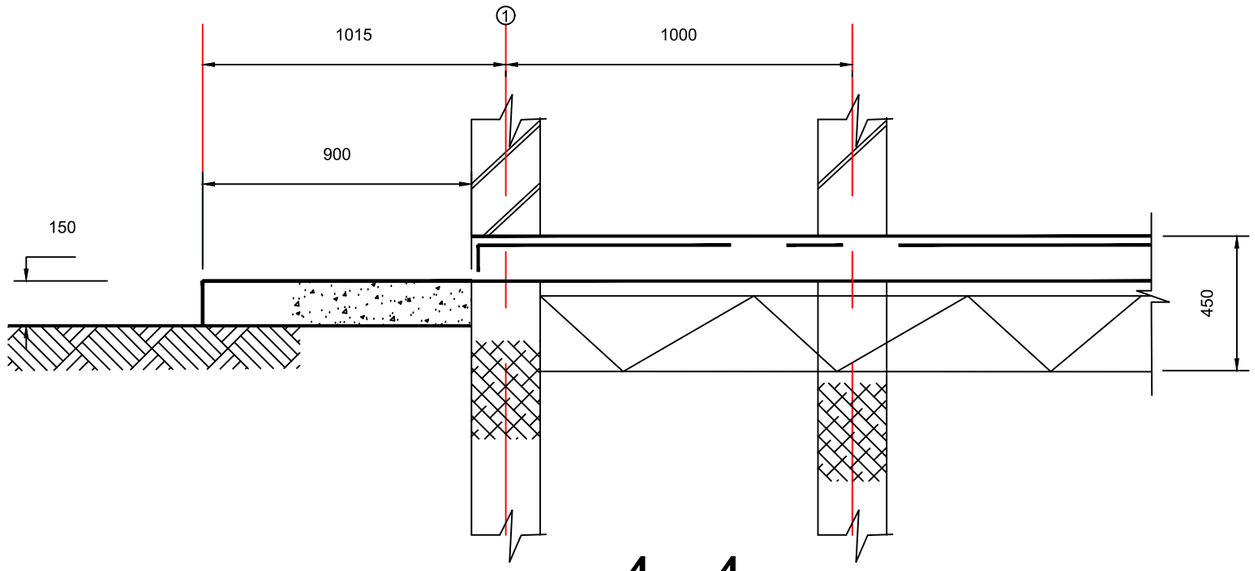

4 - 4

CLIENT	PROJECT	DRG. TITLE
Alh. AHMED JIBRIL AHMED	PROPOSED RESIDENTIAL ONE BEDROOM BLOCK OF FLAT, MABUSHI	SECTION THROUGH GROUND FLOOR

MARK	DATE	MADE BY	REVISIONS

TAPES CONSTRUCTION
NO 365 SHARADA PHASE 1
KANO, KANO STATE

JOB NO	A M BELLO DESIGNED	A BELLO DRAWN	005B DRG. No
FREE SCALE;	ENGR. B MAI CHECKED;	OCTOBER, 2020 DATE;	01 REV.

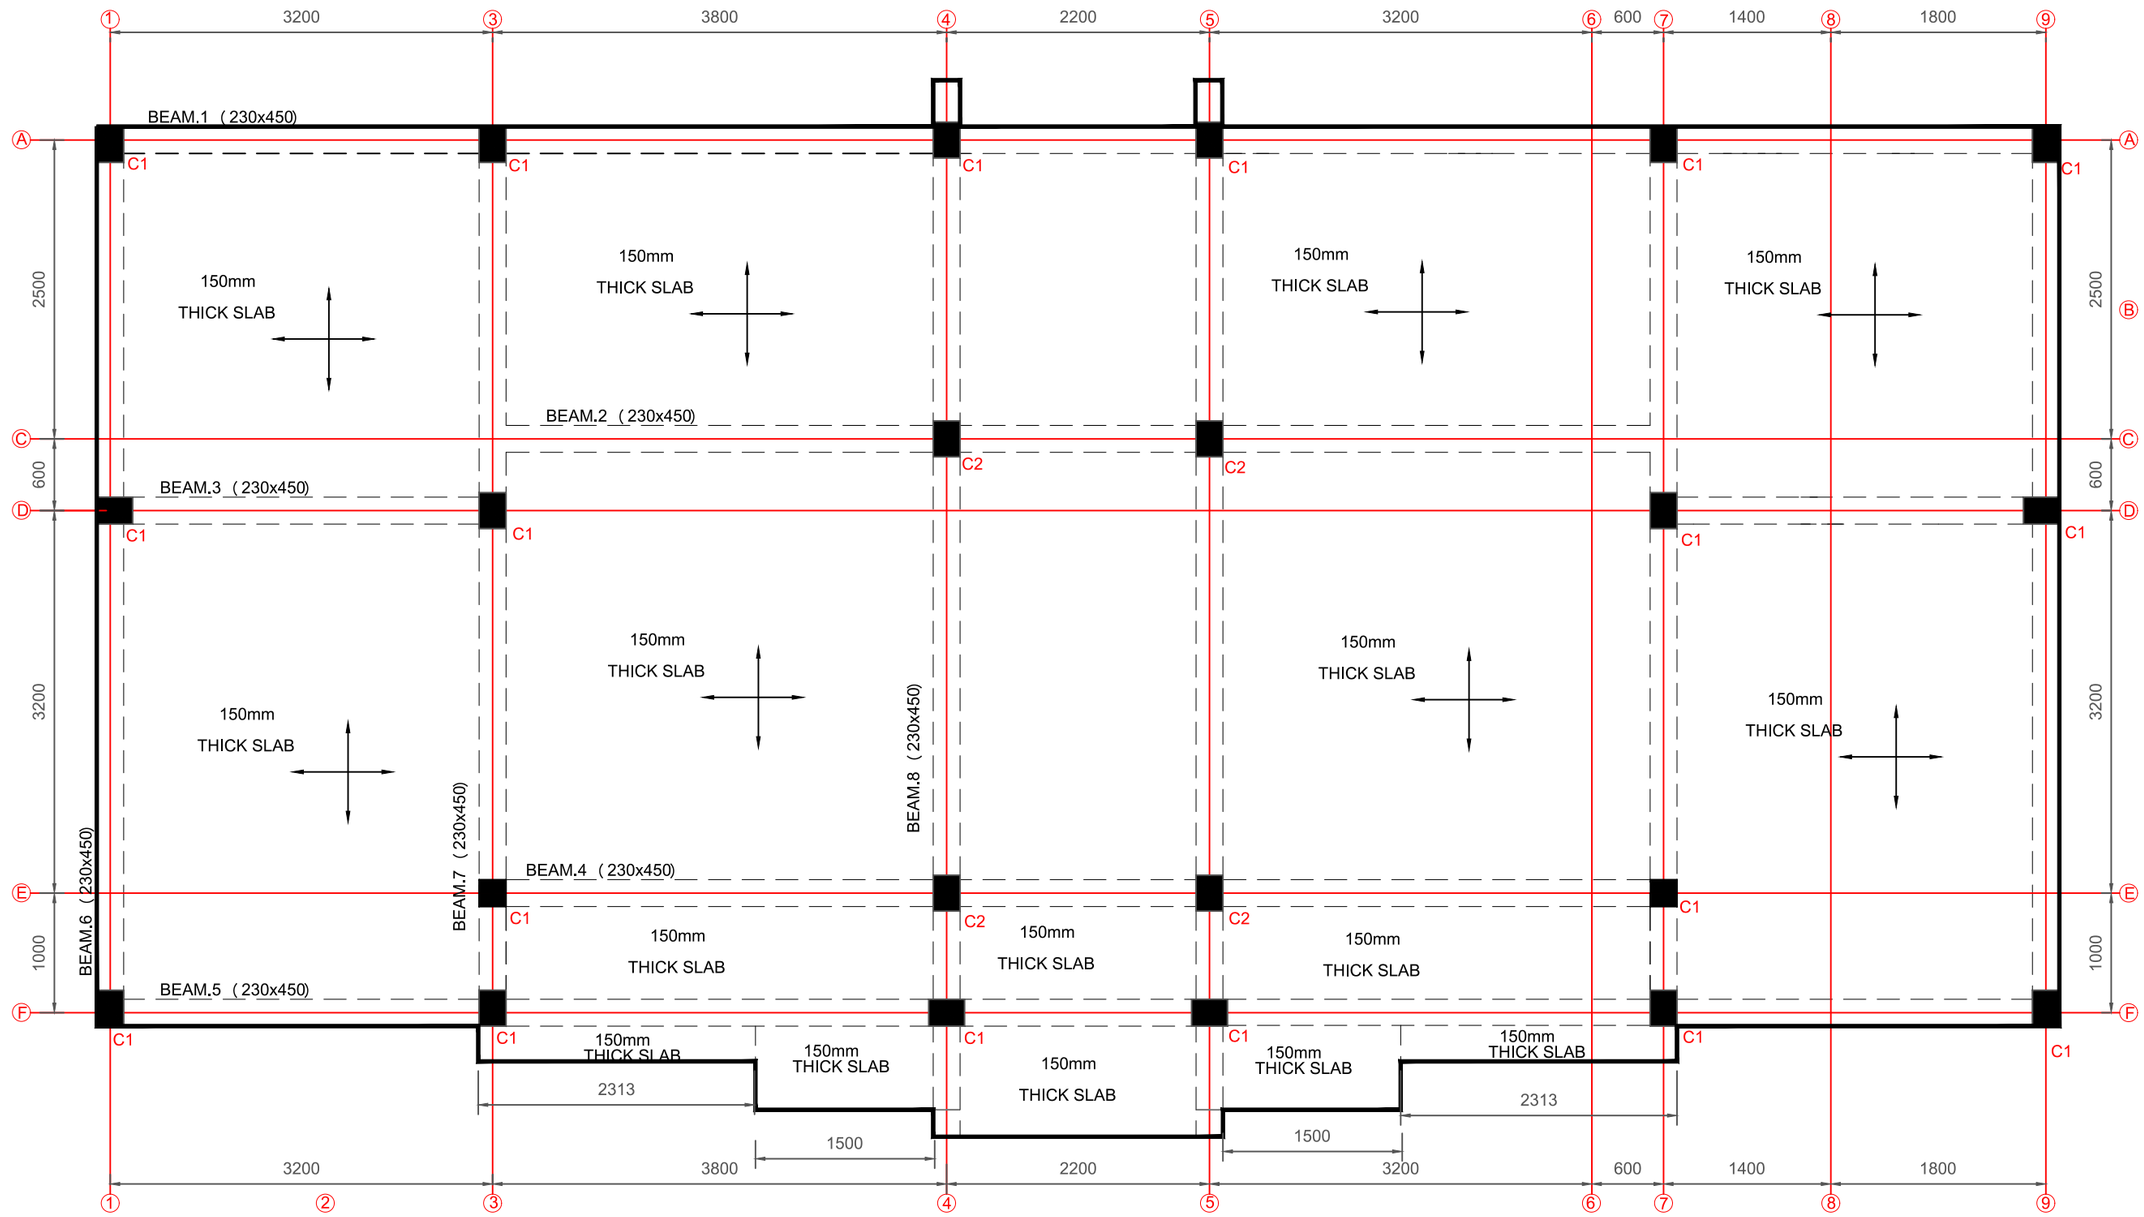

TYPICAL FIRST, SENCOND AND THIRD FLOOR LAYOUT

CLIENT	PROJECT	DRG. TITLE
Alh. AHMED JIBRIL AHMED	PROPOSED RESIDENTIAL ONE BEDROOM BLOCK OF FLAT, MABUSHI	FLOOR BEAMS AND SLABS LAYOUT

MARK	DATE	MADE BY	REVISIONS

TAPES CONSTRUCTION
NO 365 SHARADA PHASE 1
KANO, KANO STATE

JOB NO	DESIGNED	DRAWN	DRG. No
	A A BINDAWA	A A BINDAWA	006
SCALE: FREE	CHECKED: ENGR. J K	DATE: JAN, 2021	REV. 001

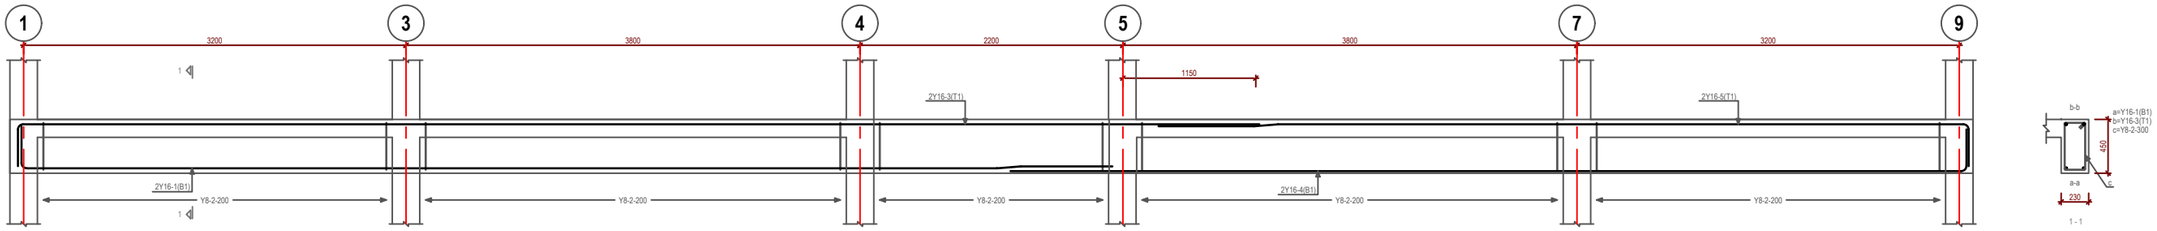

BEAM 1 (230x450)

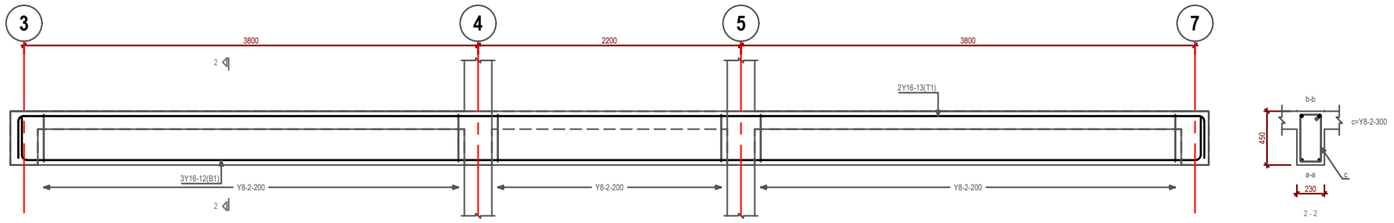

BEAM 2 (230x450)

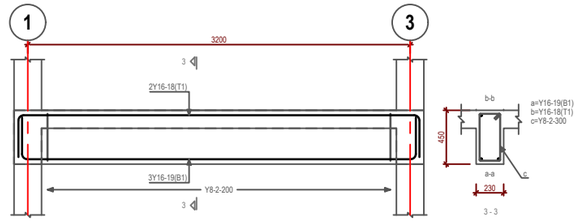

BEAM 3 (230x450)

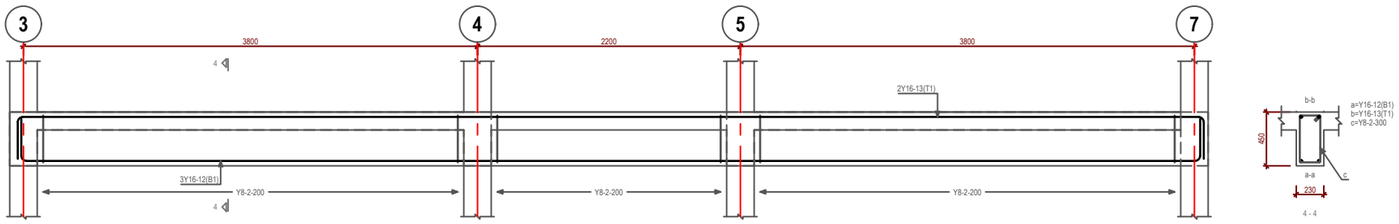

BEAM 4 (230x450)

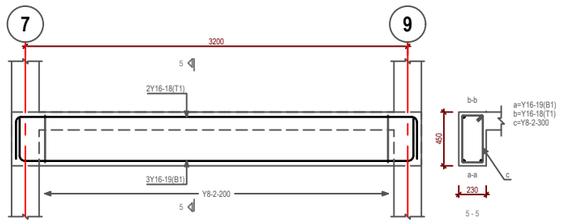

BEAM 5 (230x450)

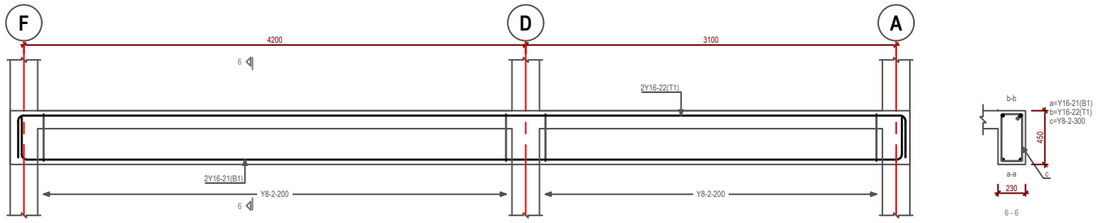

BEAM 6 (230x450)

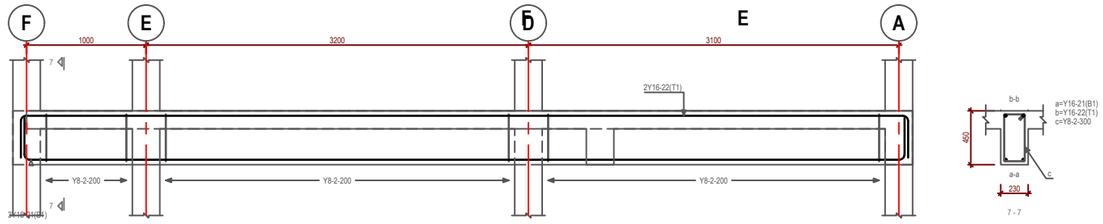

1B7 (230x450)

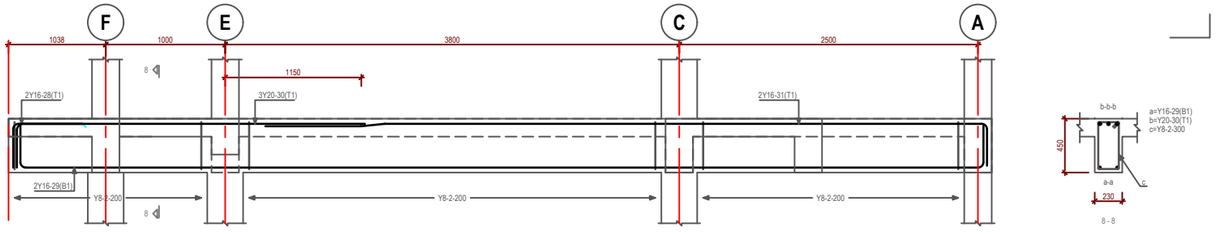

BEAM 8 (230x450)

CLIENT	PROJECT	DRG. TITLE
Alh. AHMED JIBRIL AHMED	PROPOSED RESIDENTIAL ONE BEDROOM BLOCK OF FLAT, MABUSHI	FIRST FLOOR BEAMS DETAILS

MARK	DATE	MADE BY	REVISIONS

TAPES CONSTRUCTION
NO 365 SHARADA PHASE 1
KANO, KANO STATE

JOB NO	DESIGNED	DRAWN	DRG. No
	A A BINDAWA	A A BINDAWA	007
SCALE: FREE	CHECKED: ENGR. J K	DATE: JAN, 2021	REV. 01

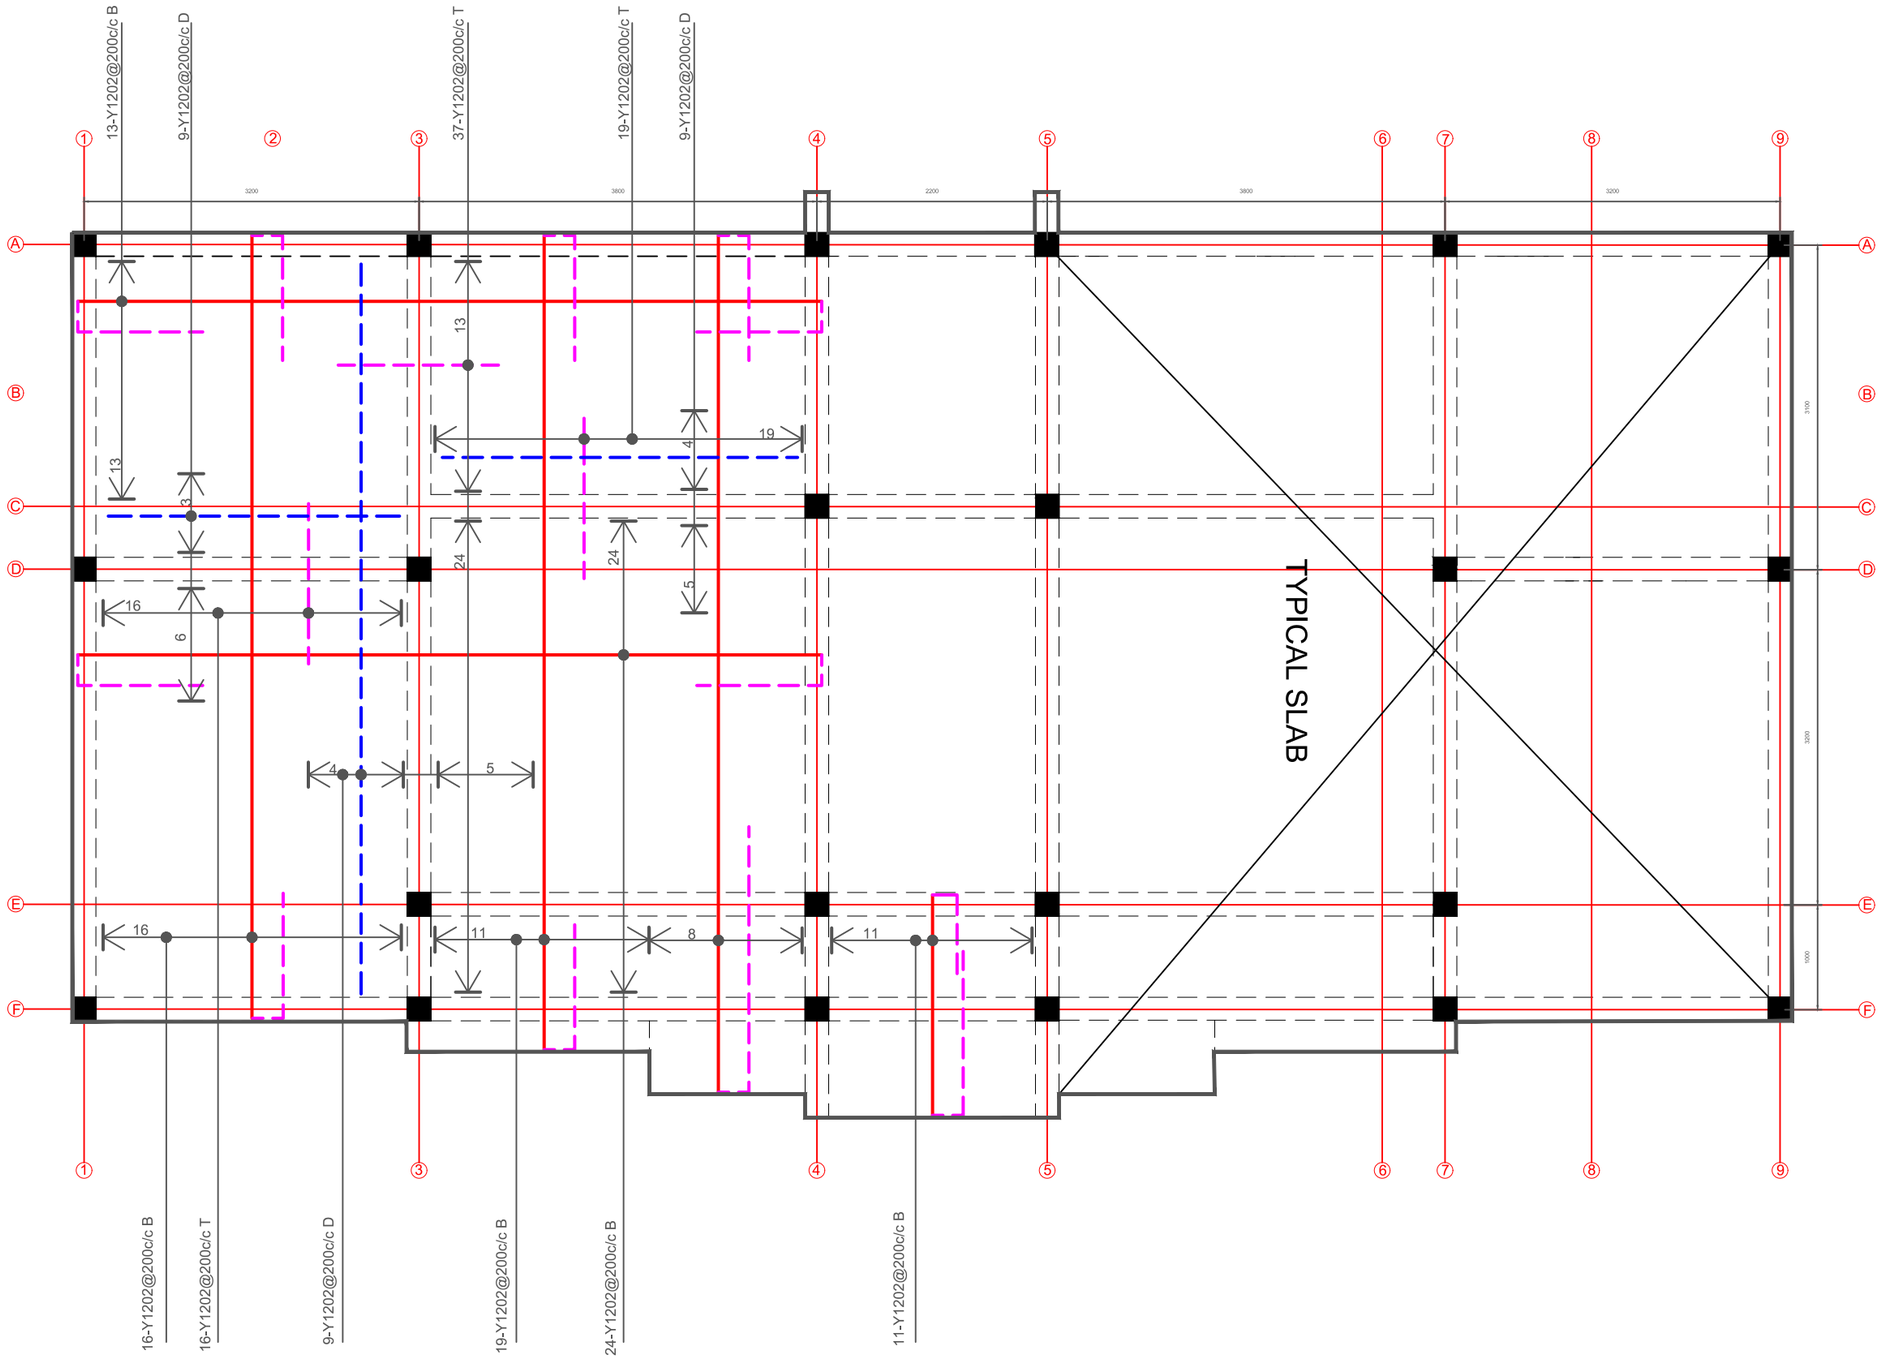

CLIENT	PROJECT	DRG. TITLE					
Alh. AHMED JIBRIL AHMED	PROPOSED RESIDENTIAL ONE BEDROOM BLOCK OF FLAT, MABUSHI	FLOOR SLAB REINF. DETAILS	MARK	DATE	MADE BY	REVISIONS	

TAPES CONSTRUCTION
NO 365 SHARADA PHASE 1
KANO, KANO STATE

JOB NO	DESIGNED	DRAWN	DRG. No
	A A BINDAWA	A A BINDAWA	008
SCALE: FREE	CHECKED: ENGR. J K	DATE: JAN, 2021	REV. 01

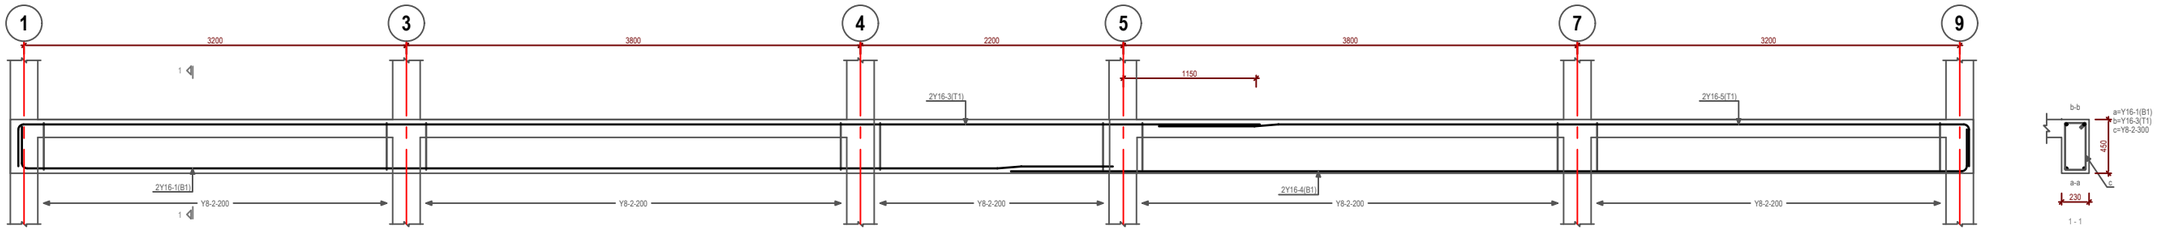

BEAM 1 (230x450)

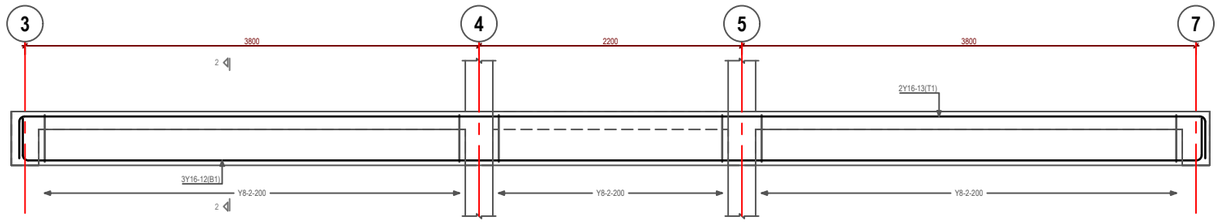

BEAM 2 (230x450)

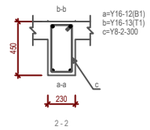

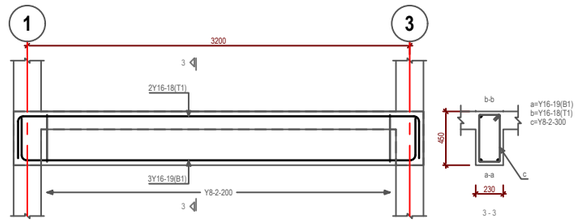

BEAM 3 (230x450)

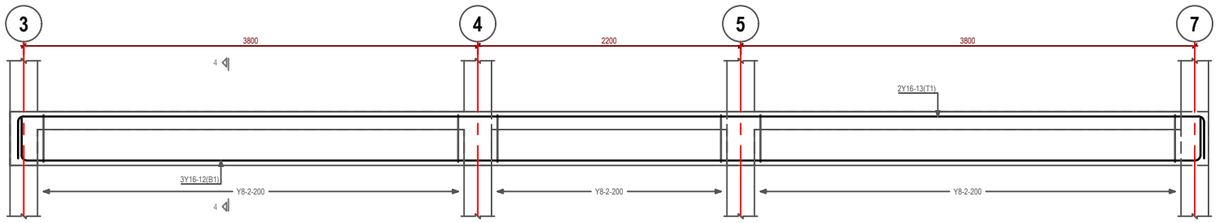

BEAM 4 (230x450)

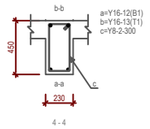

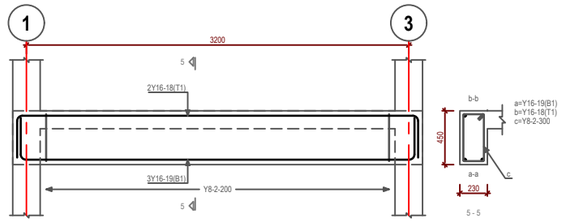

BEAM 5 (230x450)

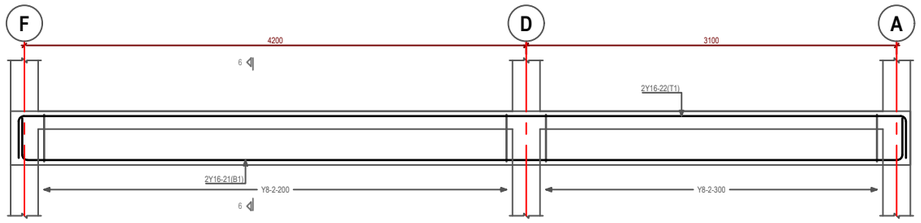

BEAM 6 (230x450)

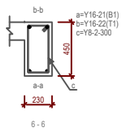

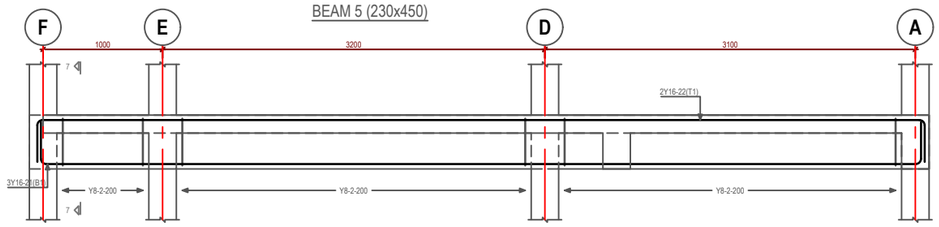

BEAM 7 (230x450)

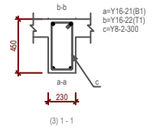

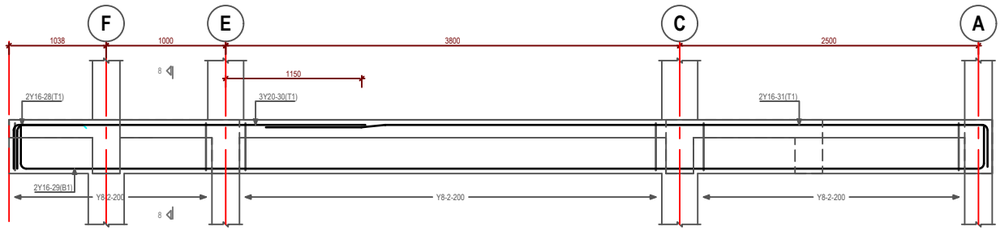

BEAM 8 (230x450)

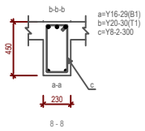

CLIENT	PROJECT	DRG. TITLE
Alh. AHMED JIBRIL AHMED	PROPOSED RESIDENTIAL ONE BEDROOM BLOCK OF FLAT, MABUSHI	SECOND FLOOR BEAMS DETAILS

MARK	DATE	MADE BY	REVISIONS

TAPES CONSTRUCTION
NO 365 SHARADA PHASE 1
KANO, KANO STATE

JOB NO	DESIGNED	DRAWN	DRG. No
	A A BINDAWA	A A BINDAWA	009
SCALE; FREE	CHECKED; ENGR. J K	DATE; JAN, 2021	REV. 01

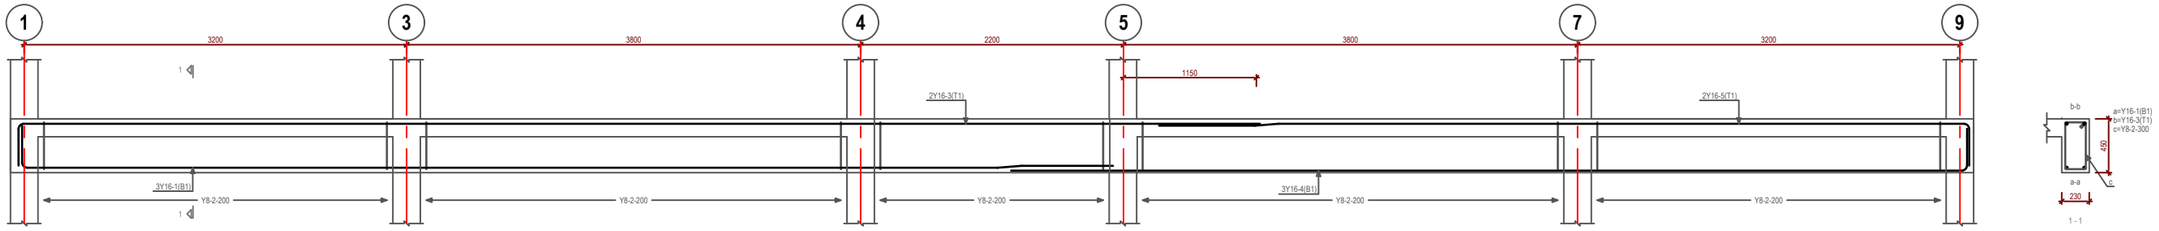

BEAM 1 (230x450)

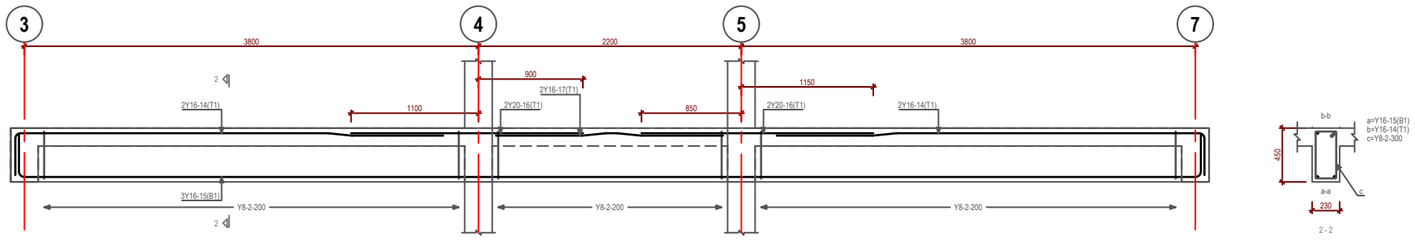

BEAM 2 (230x450)

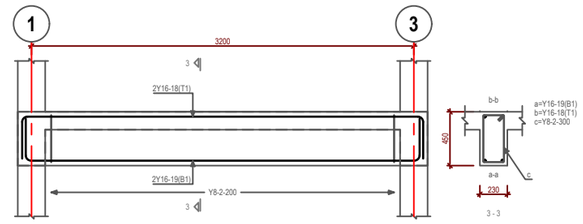

BEAM 3 (230x450)

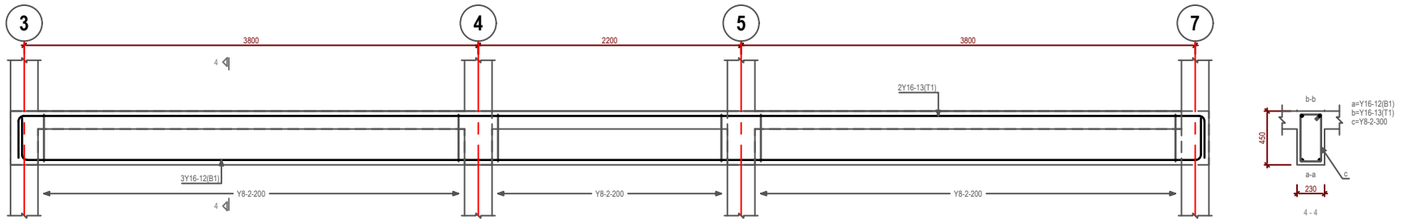

BEAM 4 (230x450)

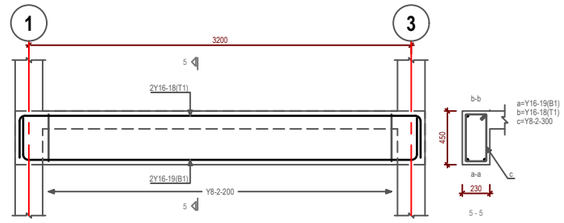

BEAM 5 (230x450)

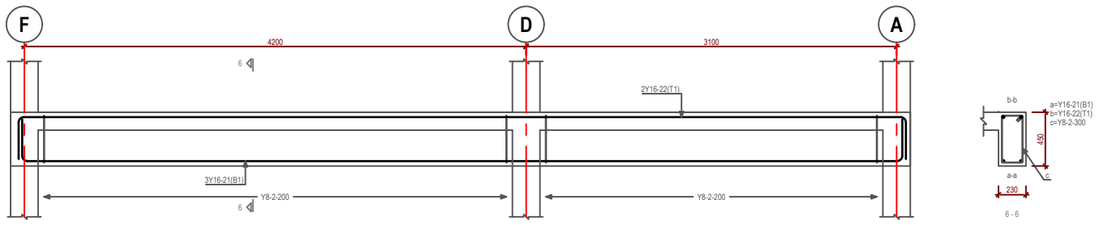

BEAM 6 (230x450)

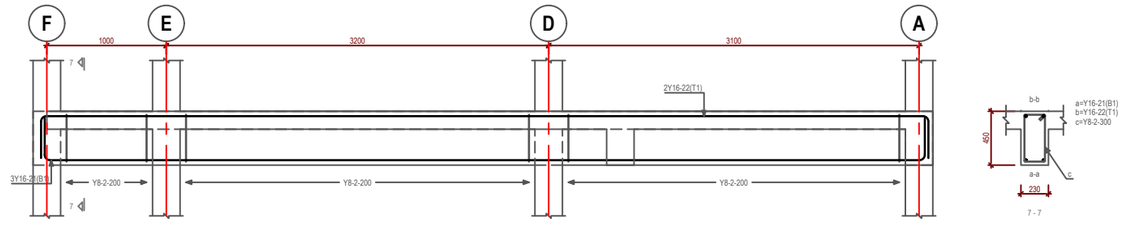

BEAM 7 (230x450)

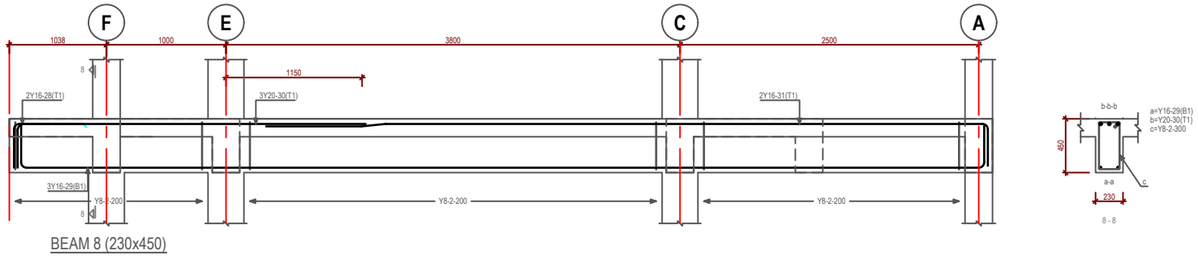

BEAM 8 (230x450)

CLIENT	PROJECT	DRG. TITLE
Alh. AHMED JIBRIL AHMED	PROPOSED RESIDENTIAL ONE BEDROOM BLOCK OF FLAT, MABUSHI	THIRD FLOOR BEAMS DETAILS

MARK	DATE	MADE BY	REVISIONS

TAPES CONSTRUCTION
NO 365 SHARADA PHASE 1
KANO, KANO STATE

JOB NO	DESIGNED	DRAWN	DRG. No
FREE	A A BINDAWA	A A BINDAWA	010
SCALE;	CHECKED; ENGR. J K	DATE; JAN, 2021	REV. 01

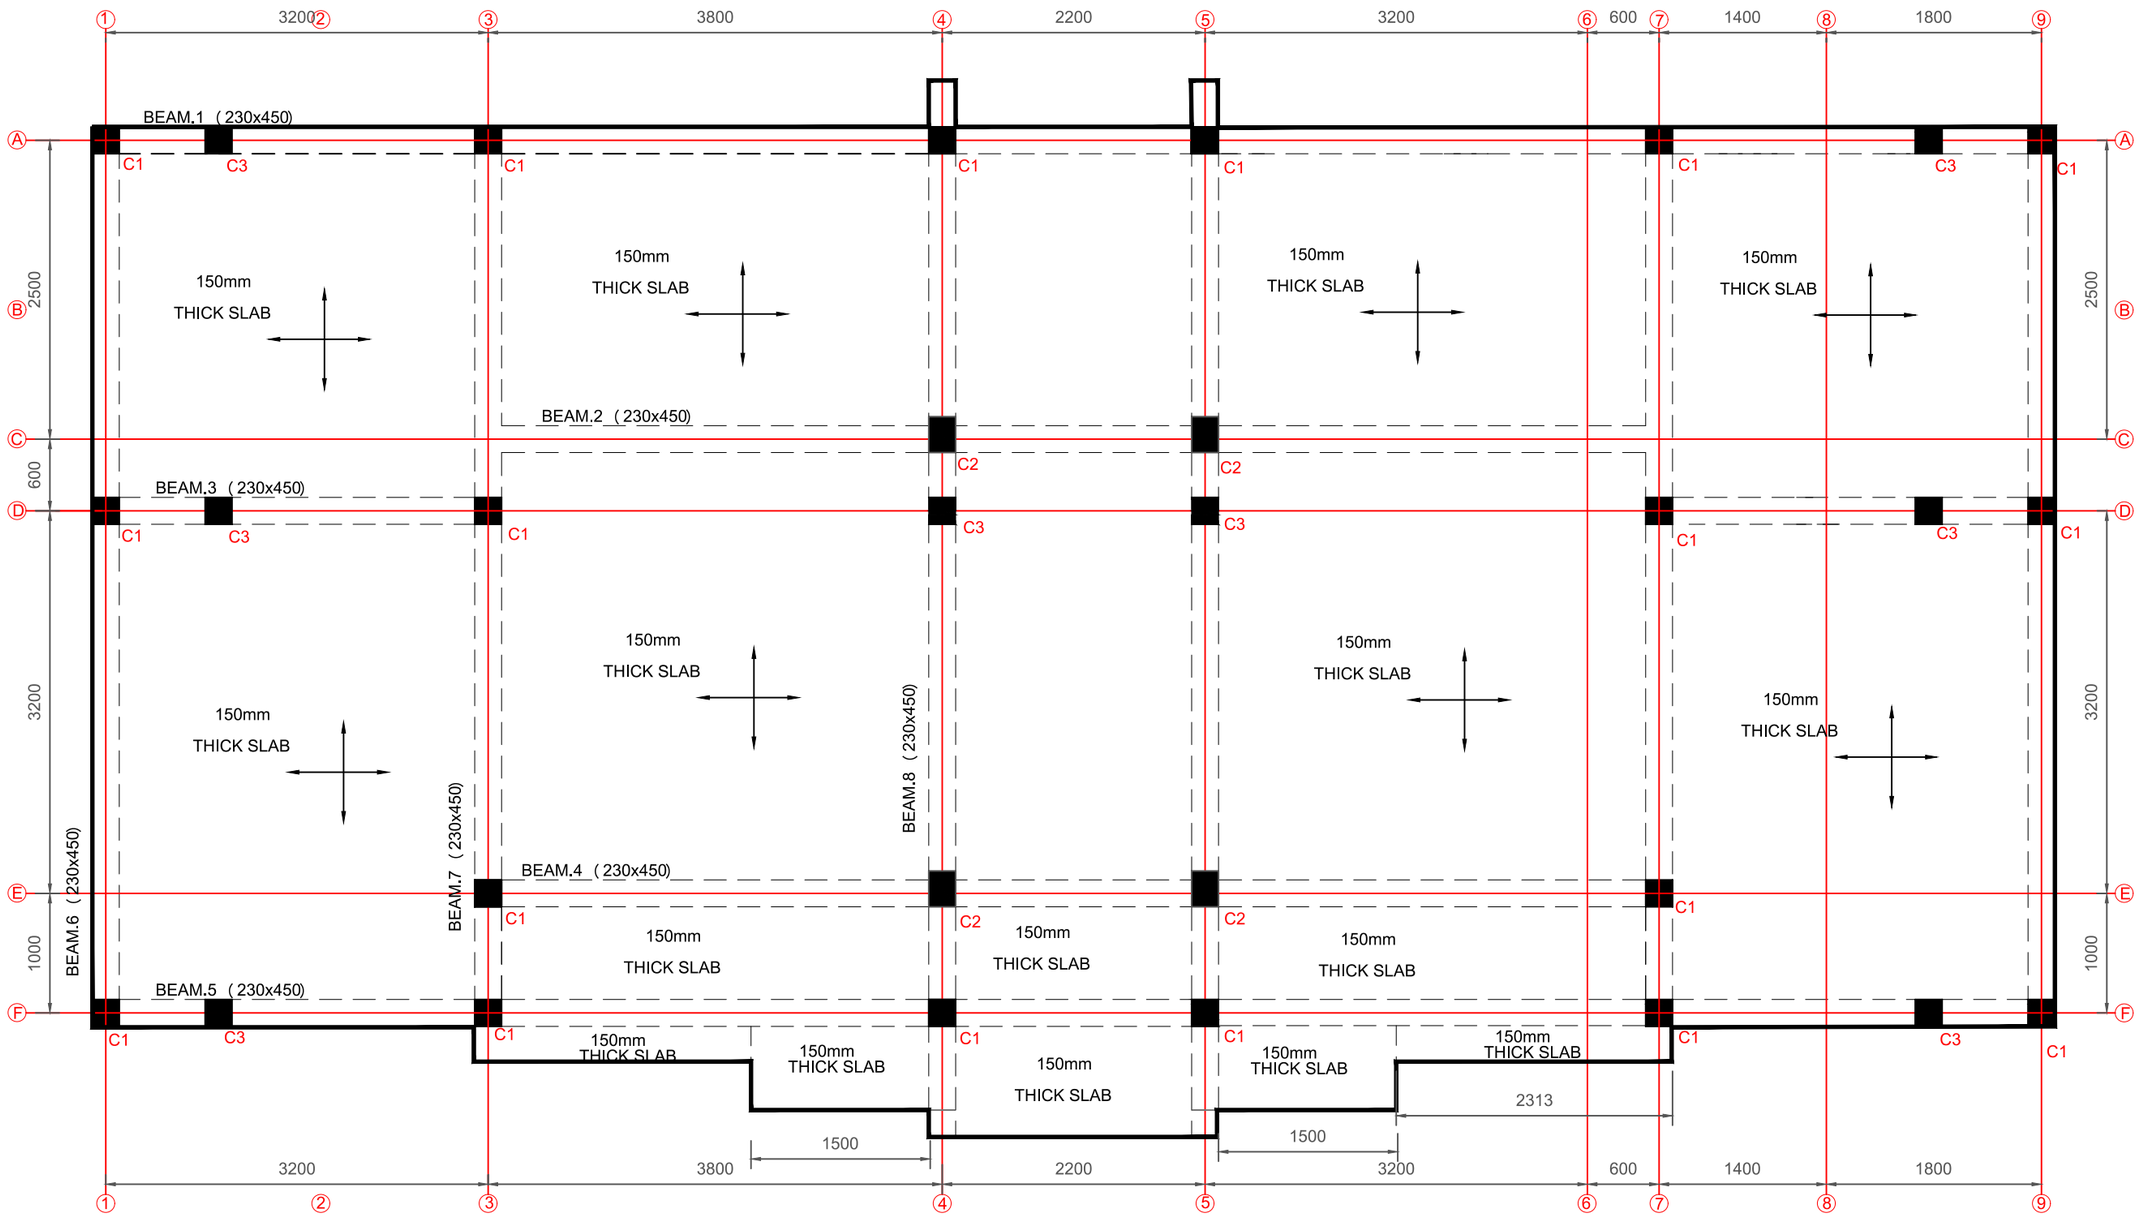

FOURTH FLOOR LAYOUT

CLIENT	PROJECT	DRG. TITLE
Alh. AHMED JIBRIL AHMED	PROPOSED RESIDENTIAL ONE BEDROOM BLOCK OF FLAT, MABUSHI	FOUTH FLOOR BEAMS AND SLABS LAYOUT

MARK DATE MADE BY REVISIONS

TAPES CONSTRUCTION
NO 365 SHARADA PHASE 1
KANO, KANO STATE

JOB NO	A A BINDAWA DESIGNED	A A BINDAWA DRAWN	011 DRG. No
FREE SCALE;	ENGR. J K CHECKED;	JAN, 2021 DATE;	01 REV.

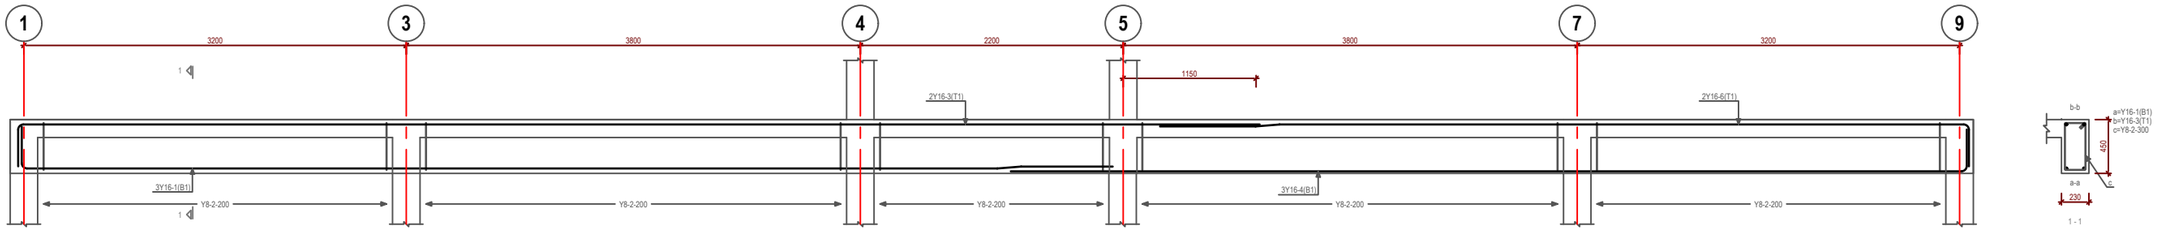

BEAM 1 (230x450)

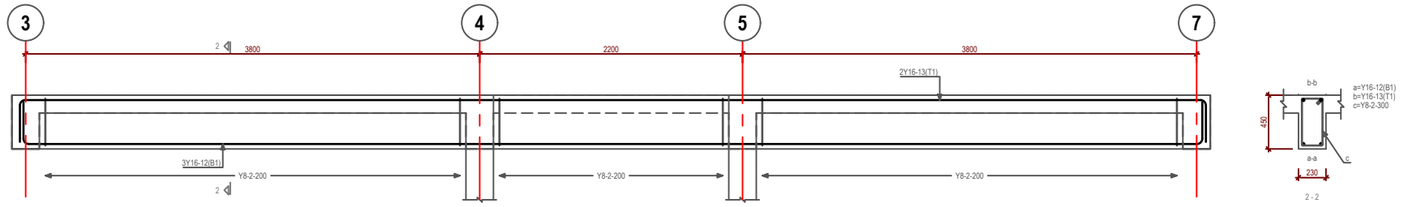

BEAM 2 (230x450)

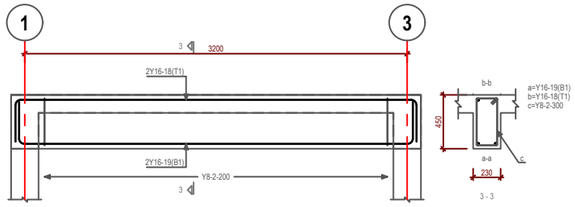

BEAM 3 (230x450)

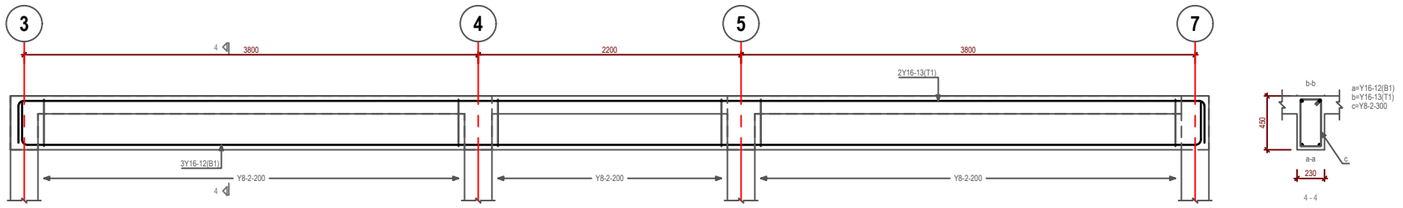

BEAM 4 (230x450)

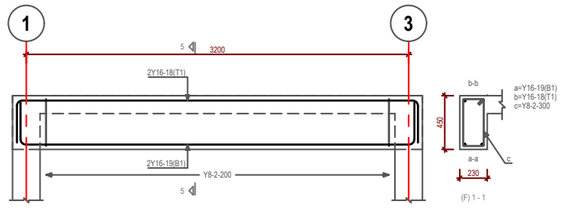

BEAM 5 (230x450)

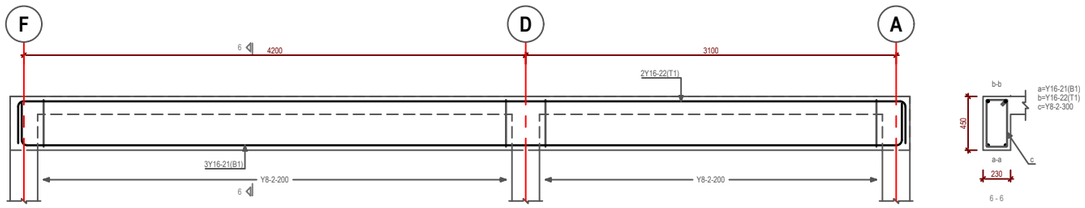

BEAM 6 (230x450)

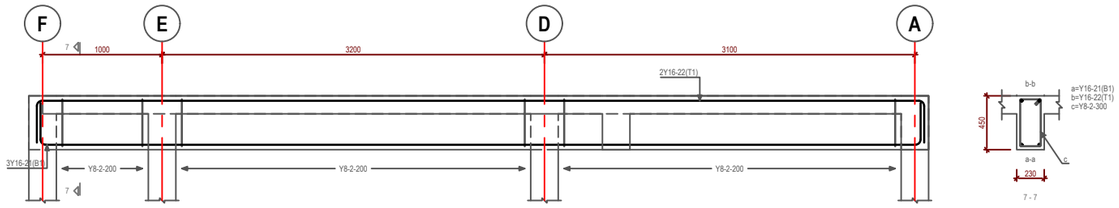

BEAM 7 (230x450)

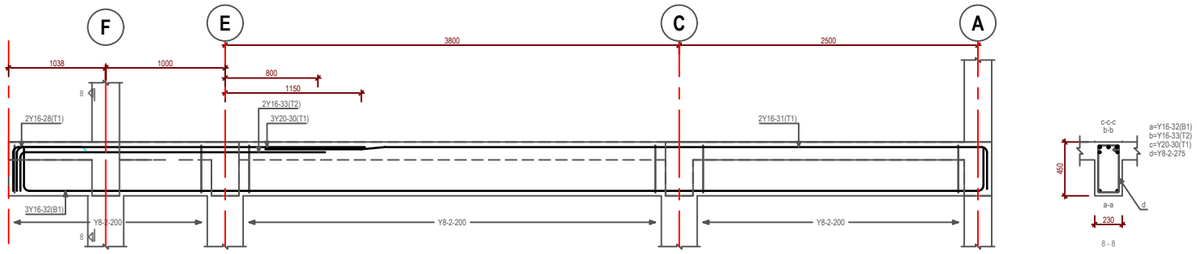

BEAM 8 (230x450)

CLIENT	PROJECT	DRG. TITLE
Alh. AHMED JIBRIL AHMED	PROPOSED RESIDENTIAL ONE BEDROOM BLOCK OF FLAT, MABUSHI	FOURTH FLOOR BEAMS DETAILS

MARK	DATE	MADE BY	REVISIONS

TAPES CONSTRUCTION
NO 365 SHARADA PHASE 1
KANO, KANO STATE

JOB NO	DESIGNED	DRAWN	DRG. No
	A A BINDAWA	A A BINDAWA	012
SCALE; FREE	CHECKED; ENGR. J K	DATE; JAN, 2021	REV. 01

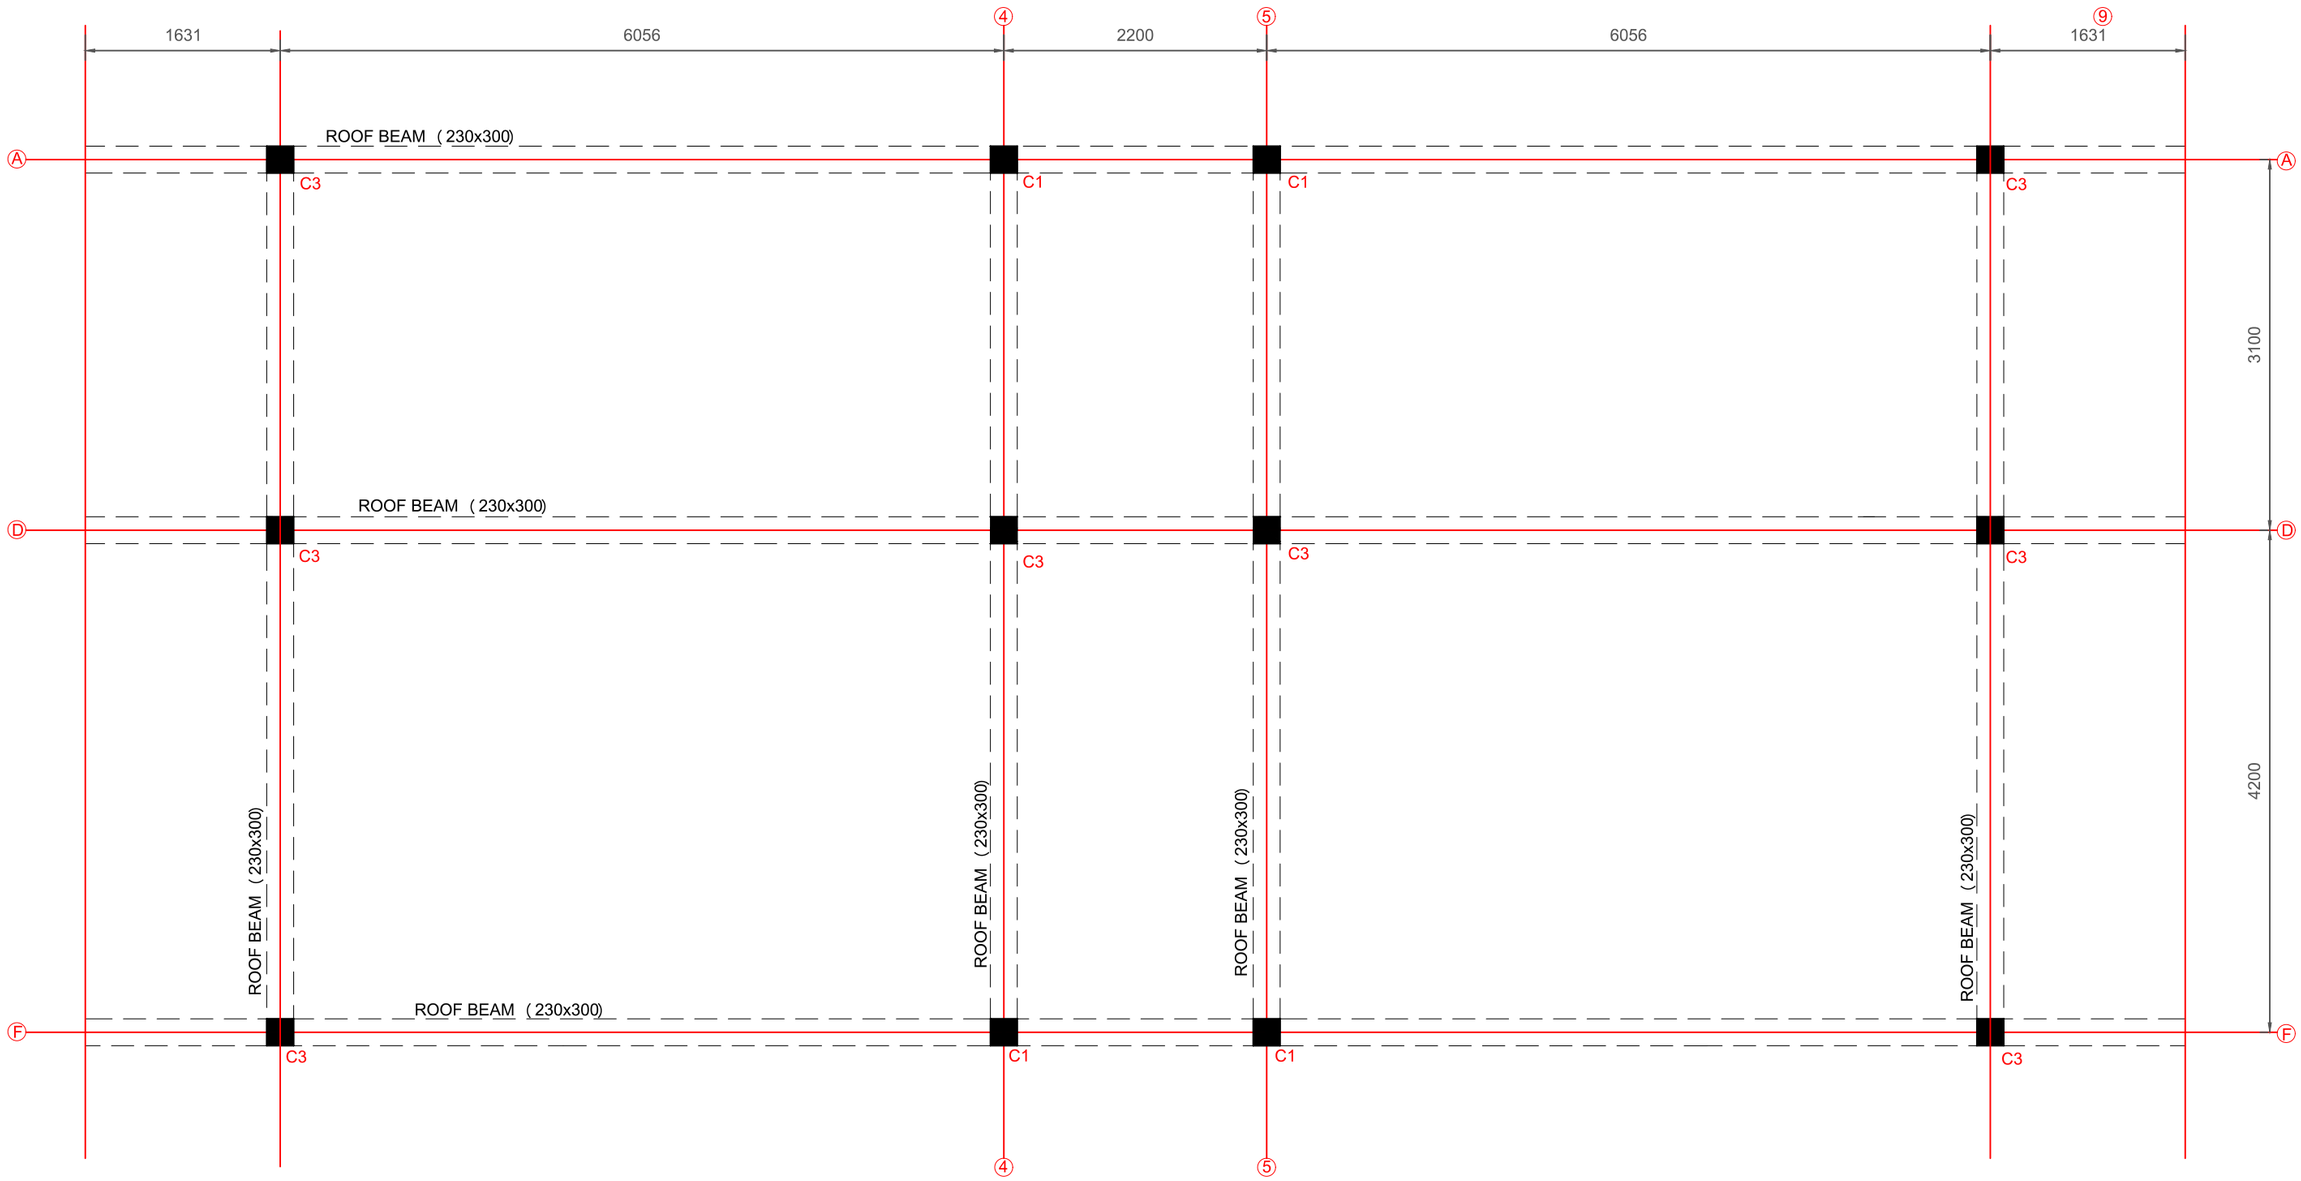

CLIENT	PROJECT	DRG. TITLE
Alh. AHMED JIBRIL AHMED	PROPOSED RESIDENTIAL ONE BEDROOM BLOCK OF FLAT, MABUSHI	ROOF BEAMS LAYOUT

MARK	DATE	MADE BY	REVISIONS

TAPES CONSTRUCTION
NO 365 SHARADA PHASE 1
KANO, KANO STATE

JOB NO	DESIGNED	DRAWN	DRG. No
	A A BINDAWA	A A BINDAWA	013
SCALE: FREE	CHECKED: ENGR. J K	DATE: JAN, 2021	REV. 01

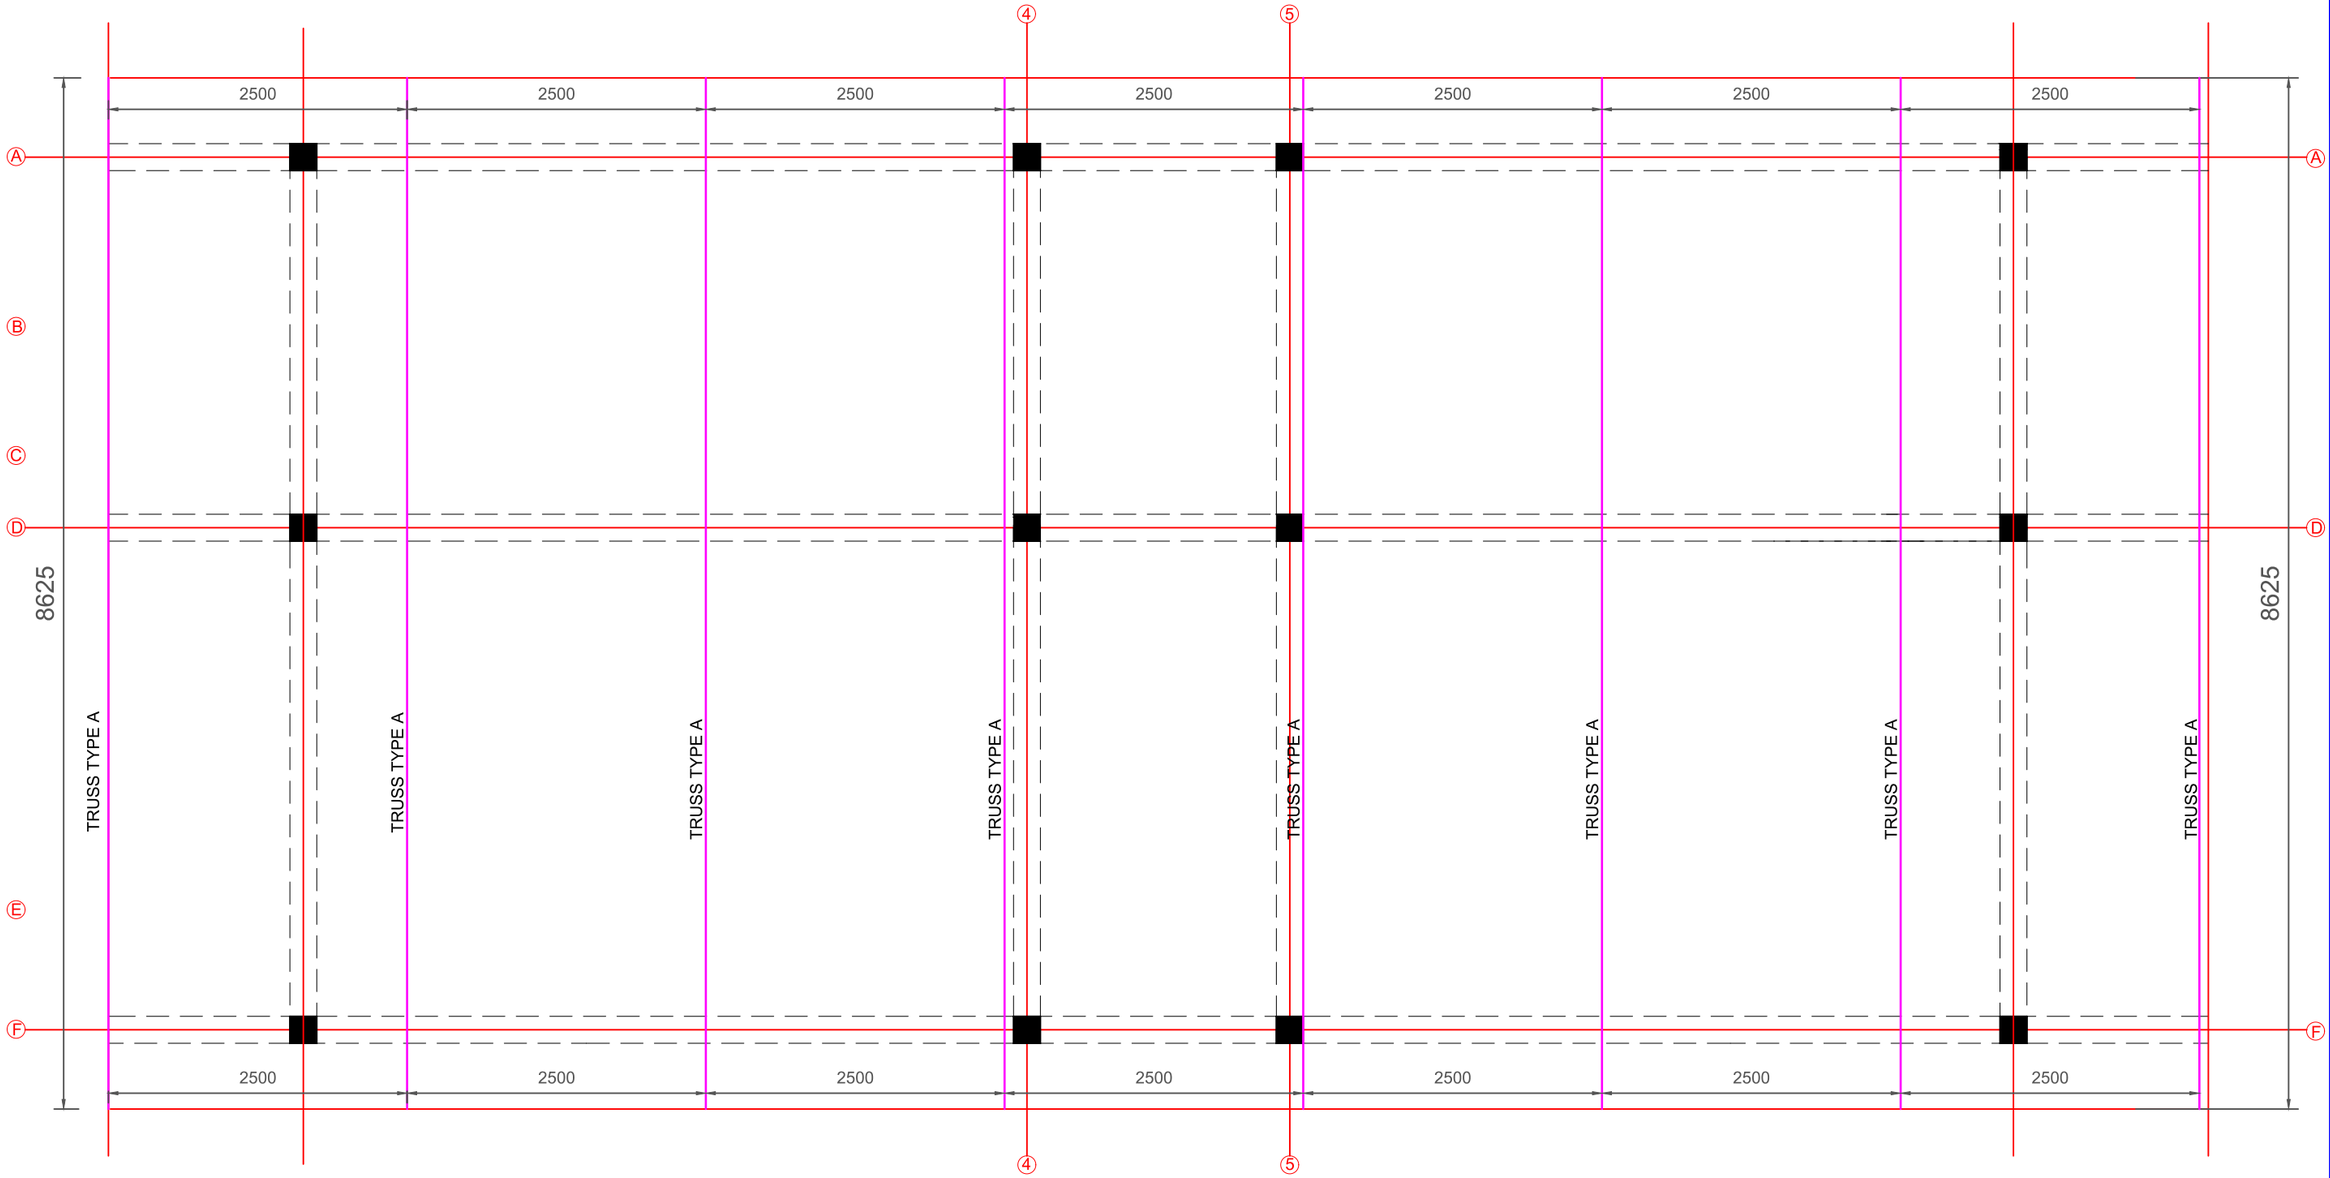

CLIENT	PROJECT	DRG. TITLE
Alh. AHMED JIBRIL AHMED	PROPOSED RESIDENTIAL ONE BEDROOM BLOCK OF FLAT, MABUSHI	ROOF TRUSS LAYOUT

MARK	DATE	MADE BY	REVISIONS

TAPES CONSTRUCTION
NO 365 SHARADA PHASE 1
KANO, KANO STATE

JOB NO	DESIGNED	DRAWN	DRG. No
	A A BINDAWA	A A BINDAWA	014
SCALE: FREE	CHECKED: ENGR. J K	DATE: JAN, 2021	REV. 01

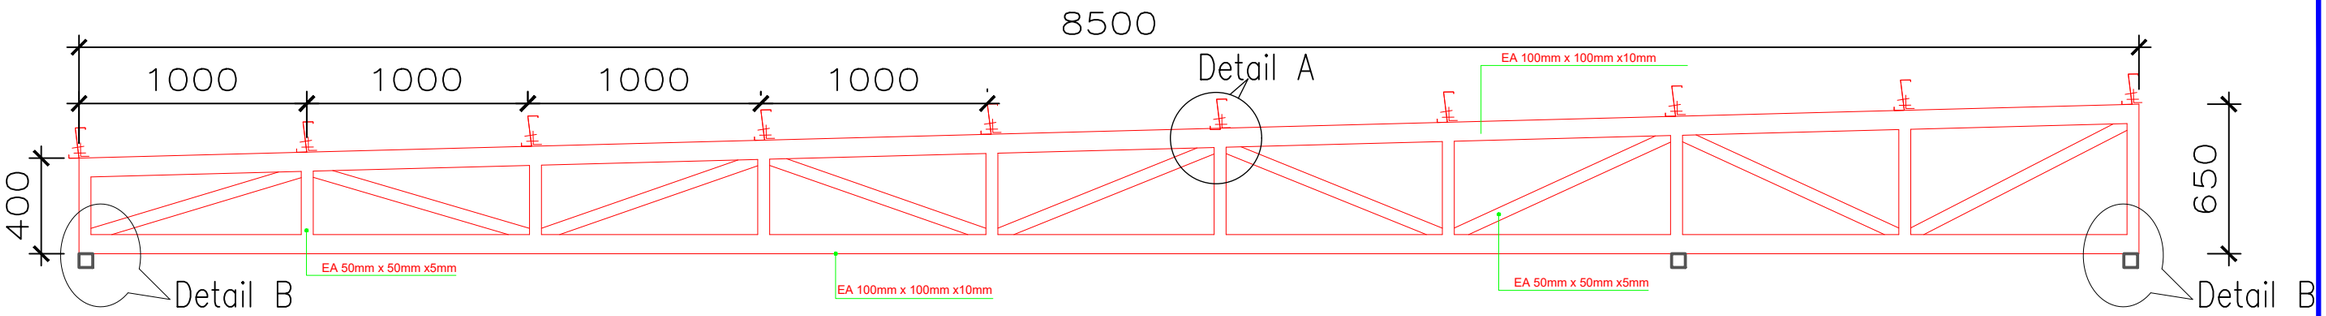

TRUSS TYPE B (1 No OFF)

NOTES

ALL WELDS ARE 6mm FILLET
ALL GUSSET PLATES ARE 6mm THICK

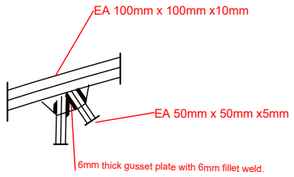

DETAIL `A`

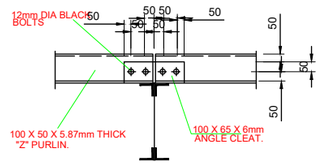

ON INTERNAL TRUSSES

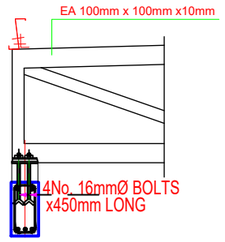

DETAIL B

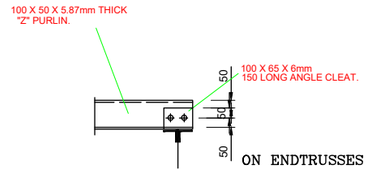

PURLIN CONNECTION DETAILS [TYPICAL]

CLIENT	PROJECT	DRG. TITLE						
Alh. AHMED JIBRIL AHMED	PROPOSED RESIDENTIAL ONE BEDROOM BLOCK OF FLAT, MABUSHI	ROOF TRUSS & CONNECTION	MARK	DATE	MADE BY	REVISIONS		

TAPES CONSTRUCTION
NO 365 SHARADA PHASE 1
KANO, KANO STATE

JOB NO	DESIGNED	DRAWN	DRG. No
	A A BINDAWA	A A BINDAWA	015
SCALE: FREE	CHECKED: ENGR. J K	DATE: JAN, 2021	REV. 01

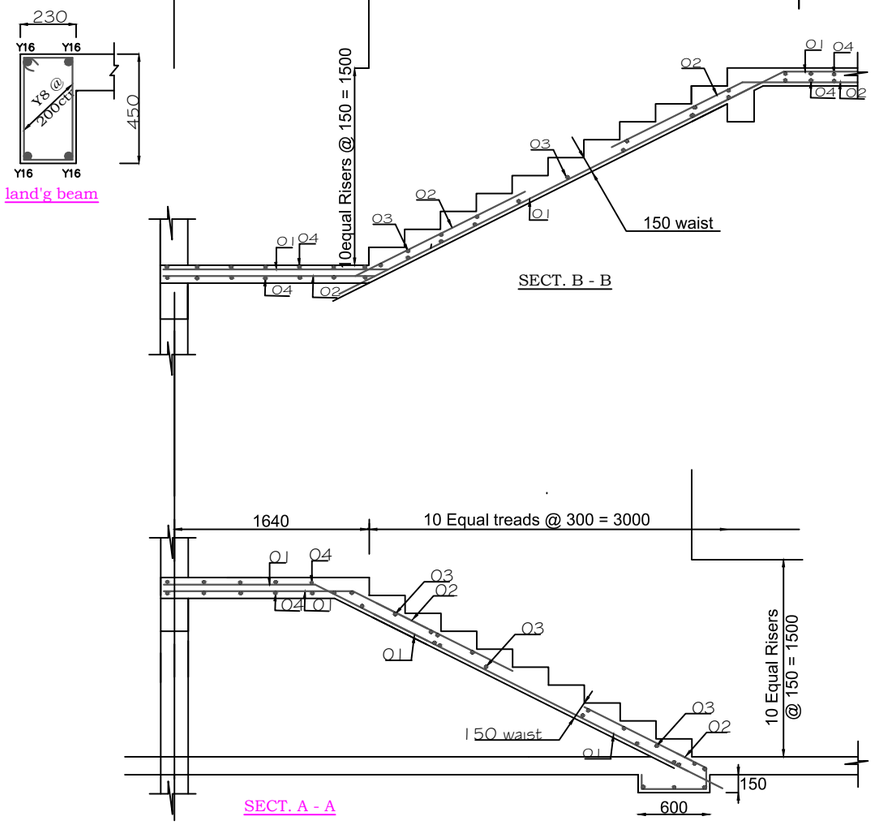

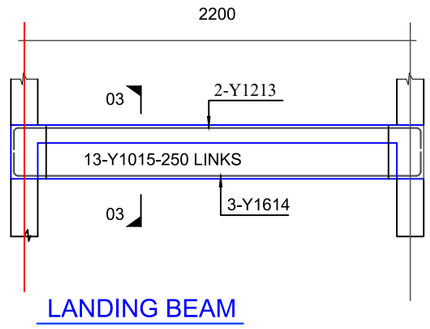

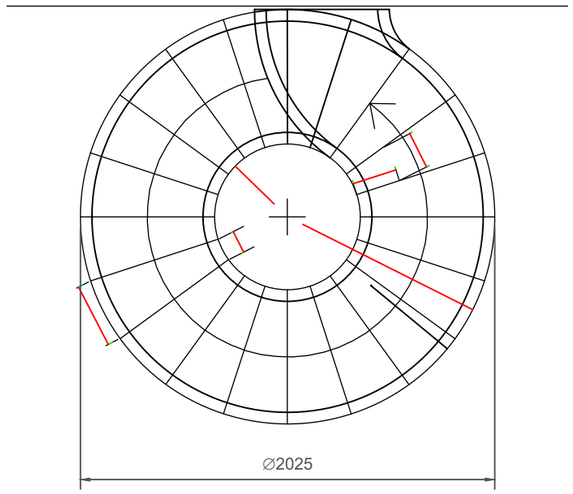

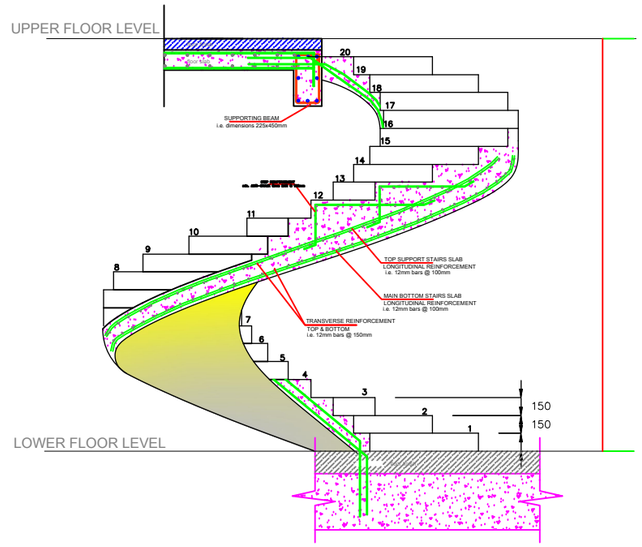

FLOOR TO FLOOR STAIR DETAILS

CLIENT	PROJECT	DRG. TITLE						
Alh. AHMED JIBRIL AHMED	PROPOSED RESIDENTIAL ONE BEDROOM BLOCK OF FLAT, MABUSHI	STAIR DETAILS				TAPES CONSTRUCTION NO 365 SHARADA PHASE 1 KANO, KANO STATE		
			MARK	DATE	MADE BY	REVISIONS	JOB NO	A M BELLO DESIGNED	A BELLO DRAWN	016 DRG. No
							FREE SCALE;	ENGR. B MAI CHECKED;	OCTOBER, 2020 DATE;	01 REV.